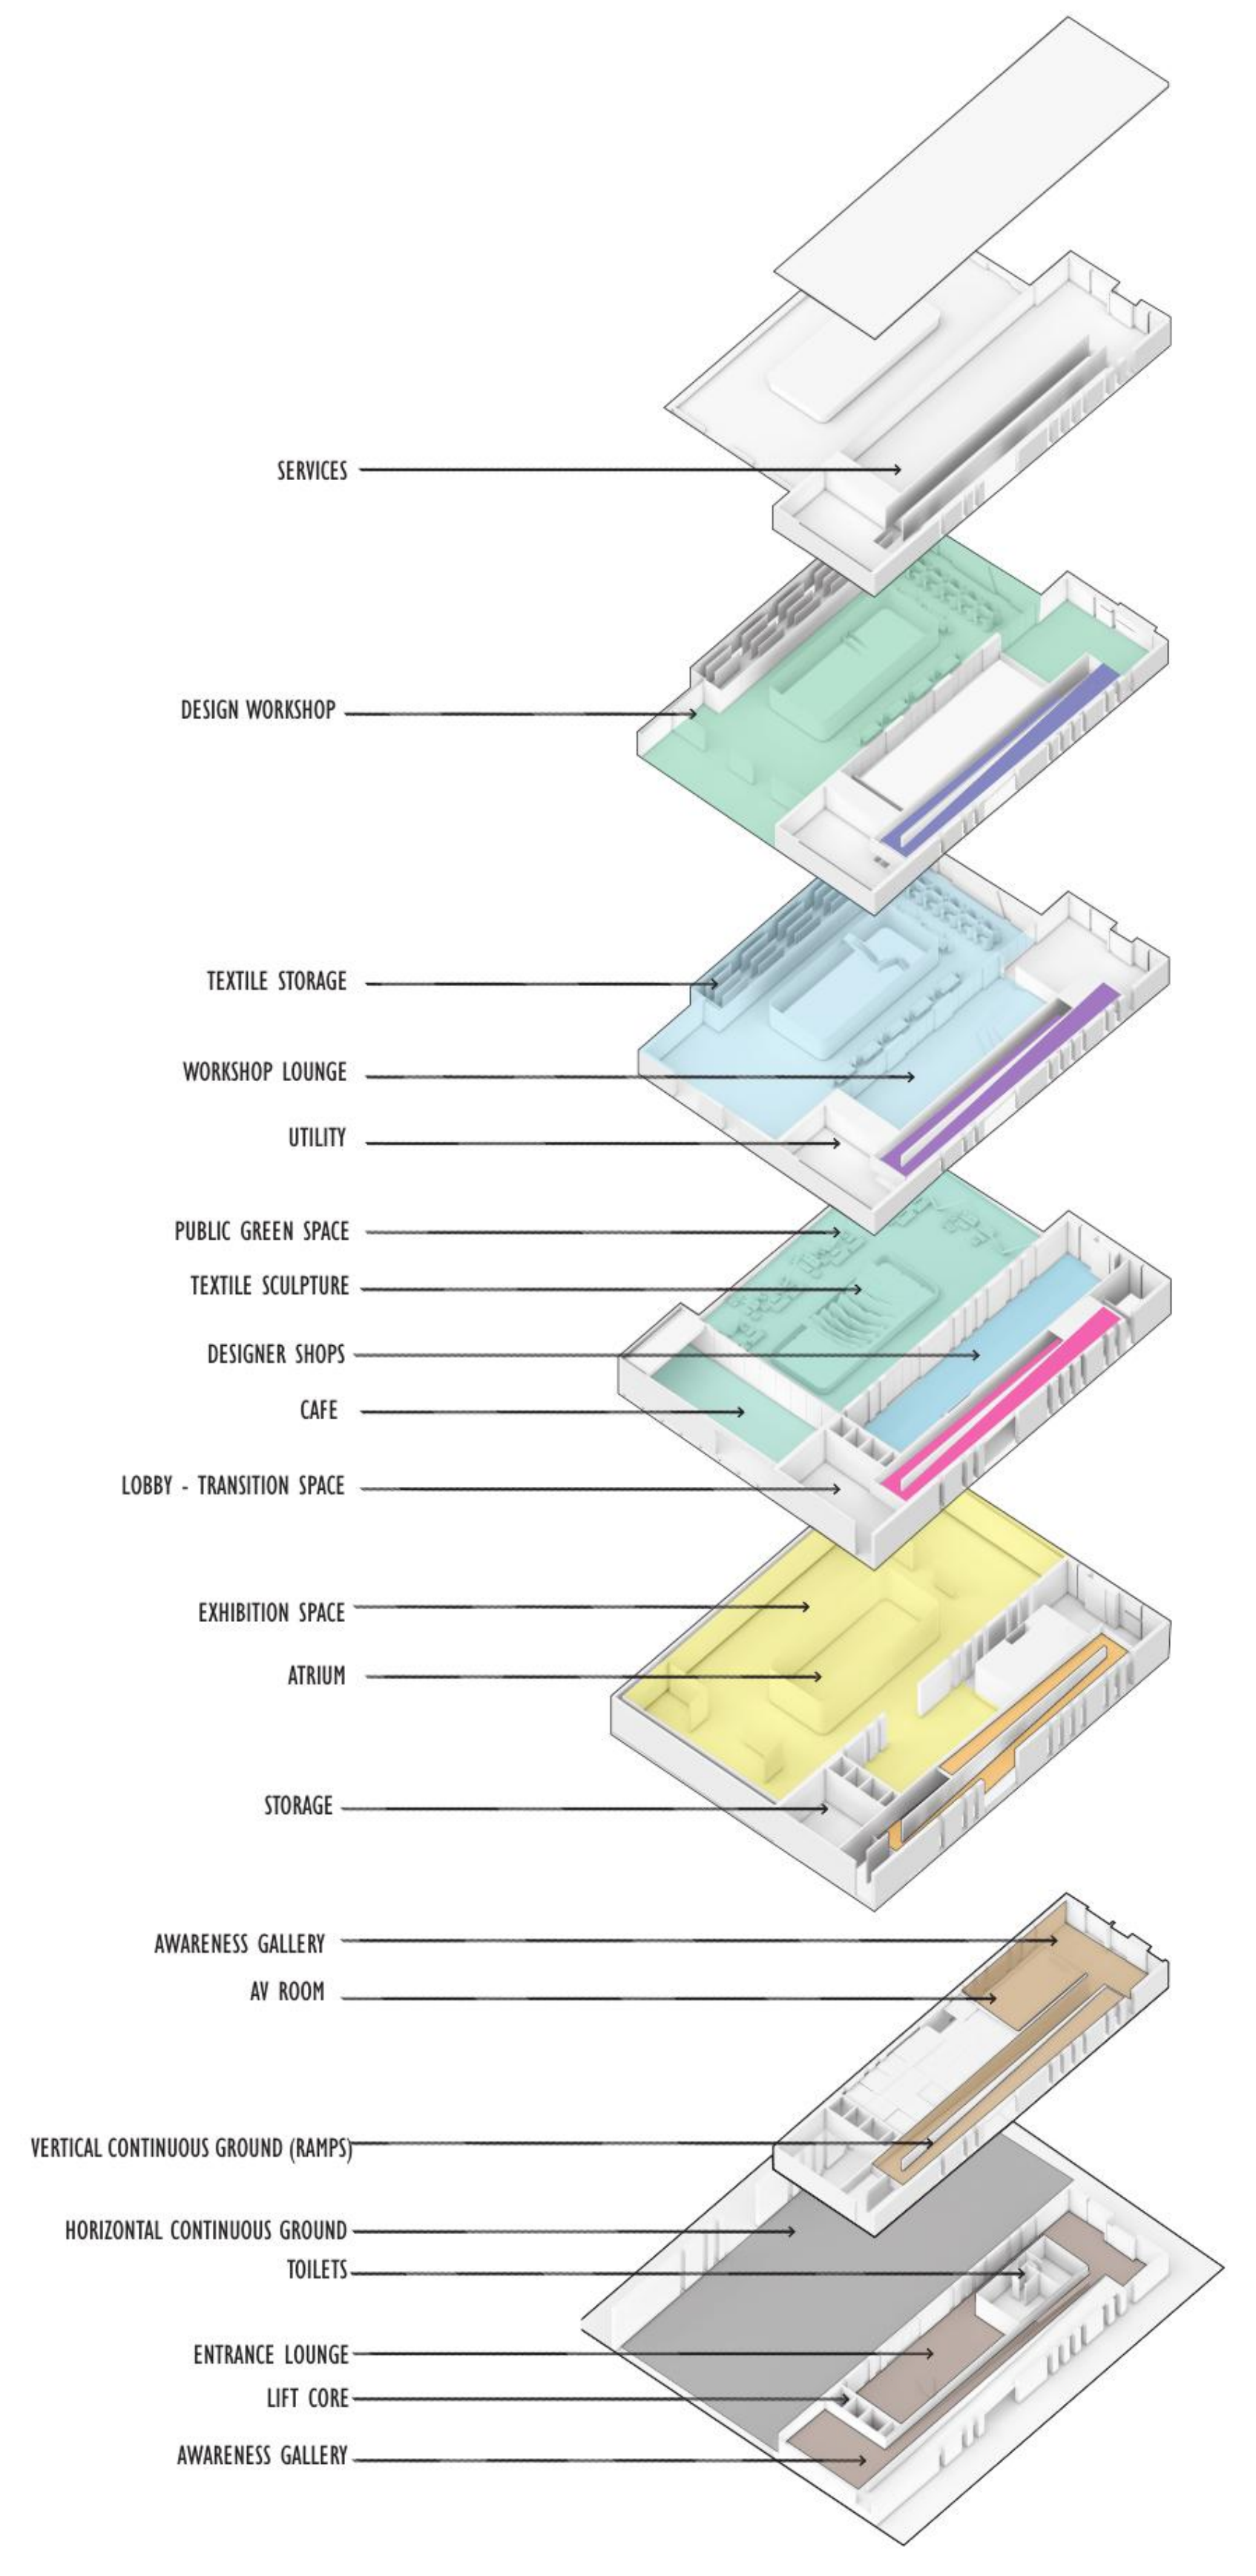
SERVICES
DESIGN WORKSHOP
TEXTILE STORAGE
WORKSHOP LOUNGE
UTILITY
PUBLIC GREEN SPACE
TEXTILE SCULPTURE
DESIGNER SHOPS
CAFE
LOBBY - TRANSITION SPACE
EXHIBITION SPACE
ATRIUM
STORAGE
AWARENESS GALLERY
AV ROOM
VERTICAL CONTINUOUS GROUND (RAMPS)
HORIZONTAL CONTINUOUS GROUND
TOILETS
ENTRANCE LOUNGE
LIFT CORE
AWARENESS GALLERY

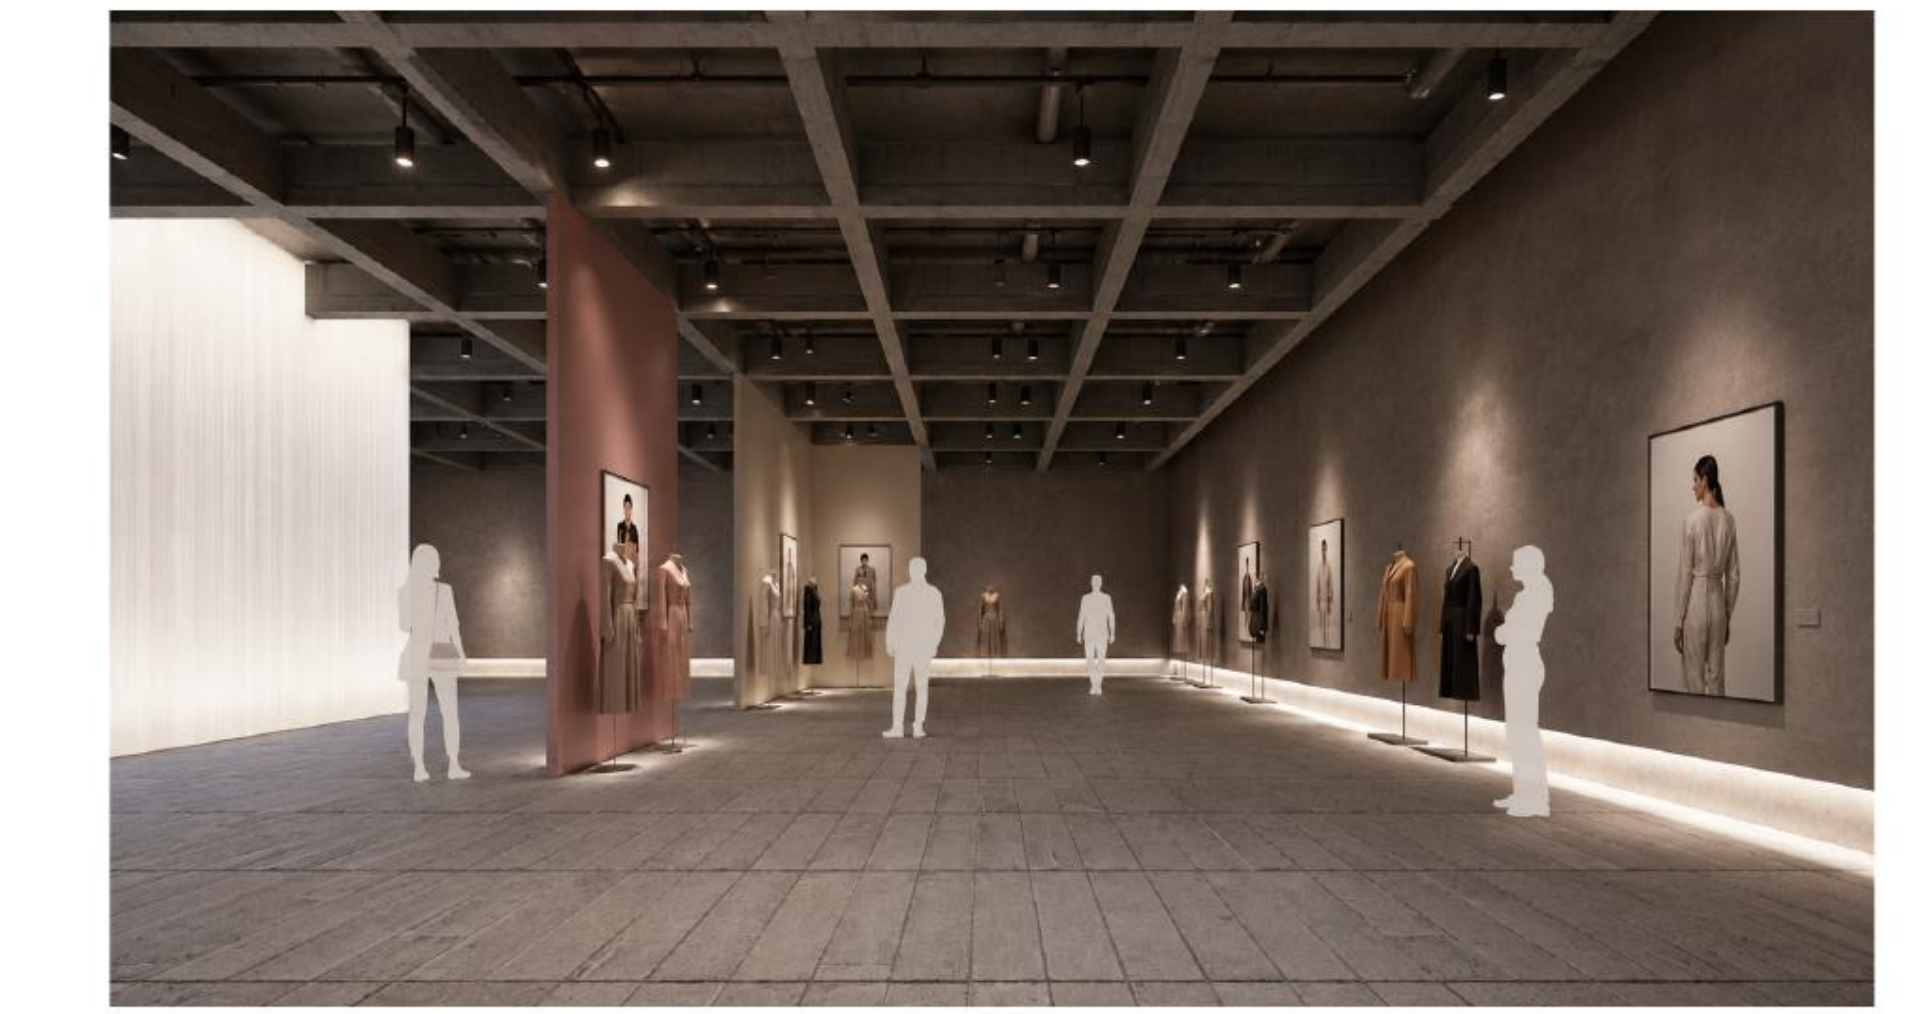

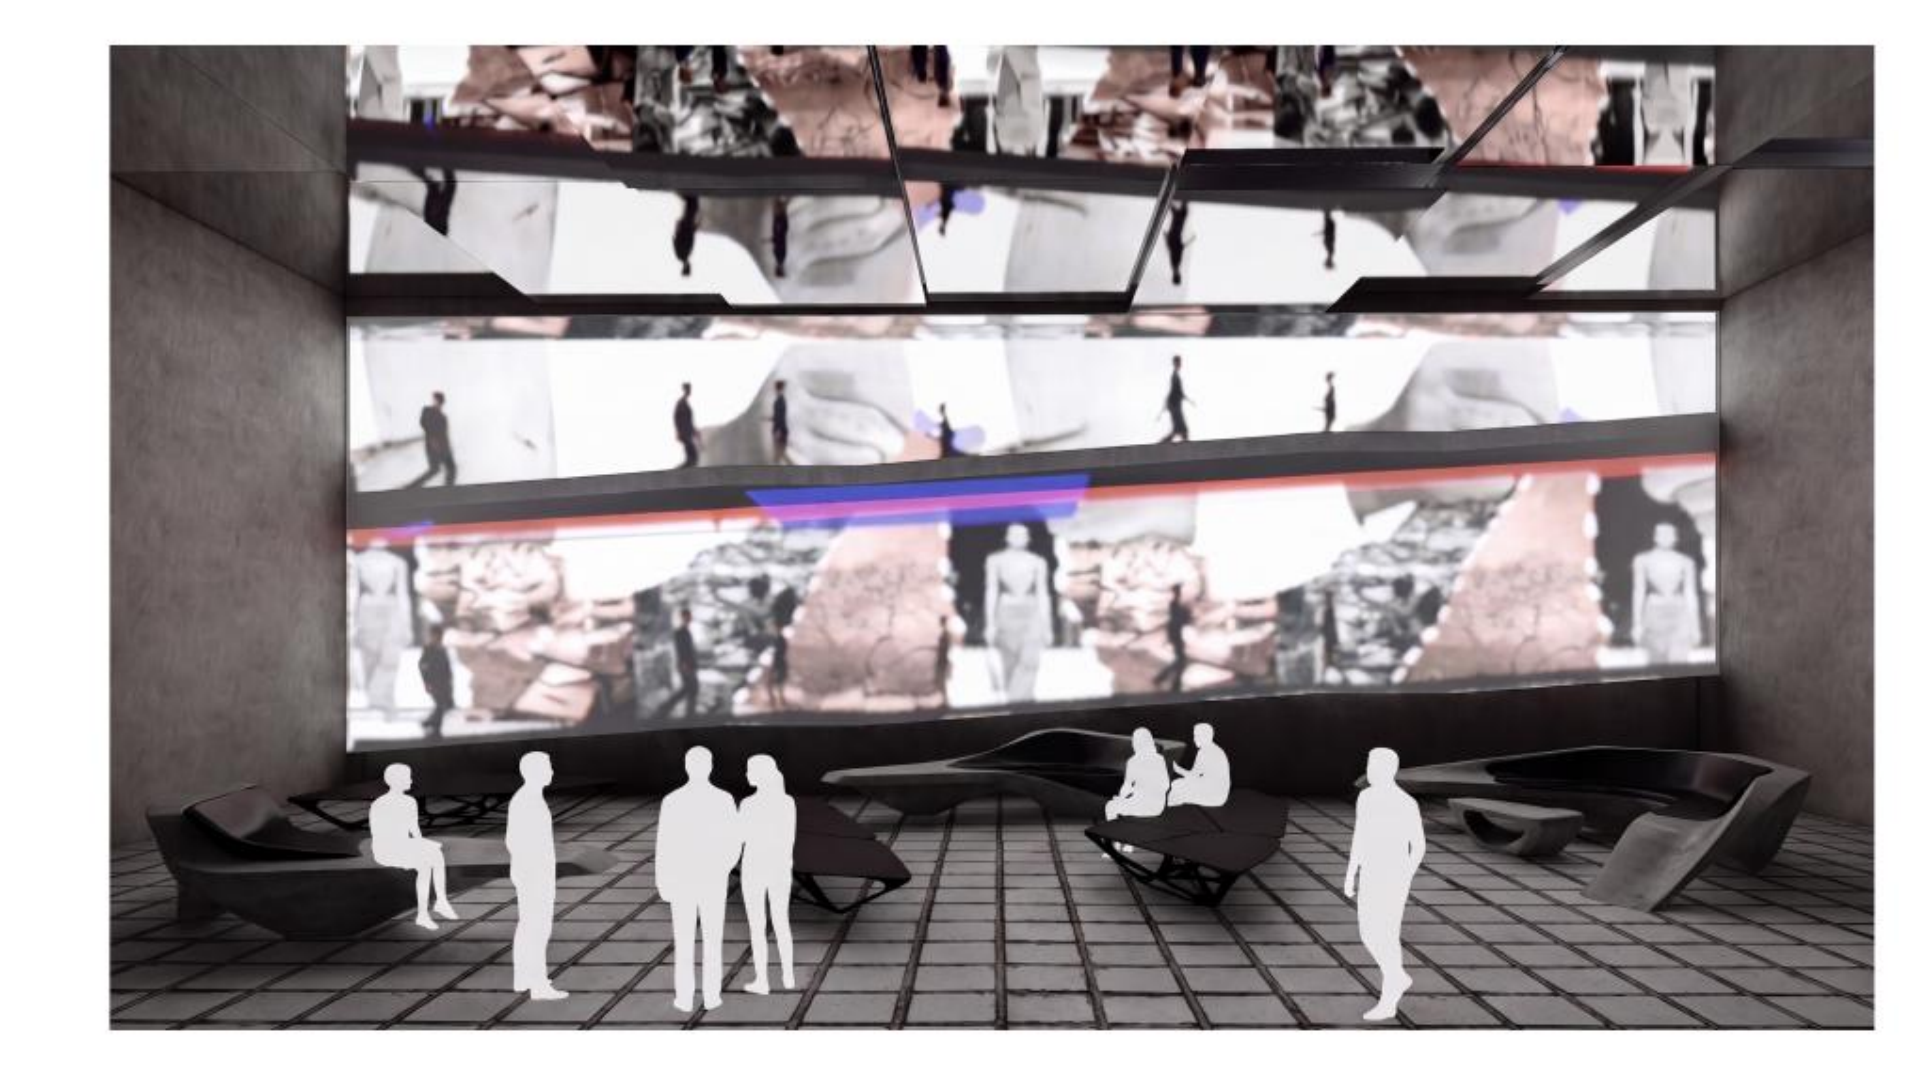

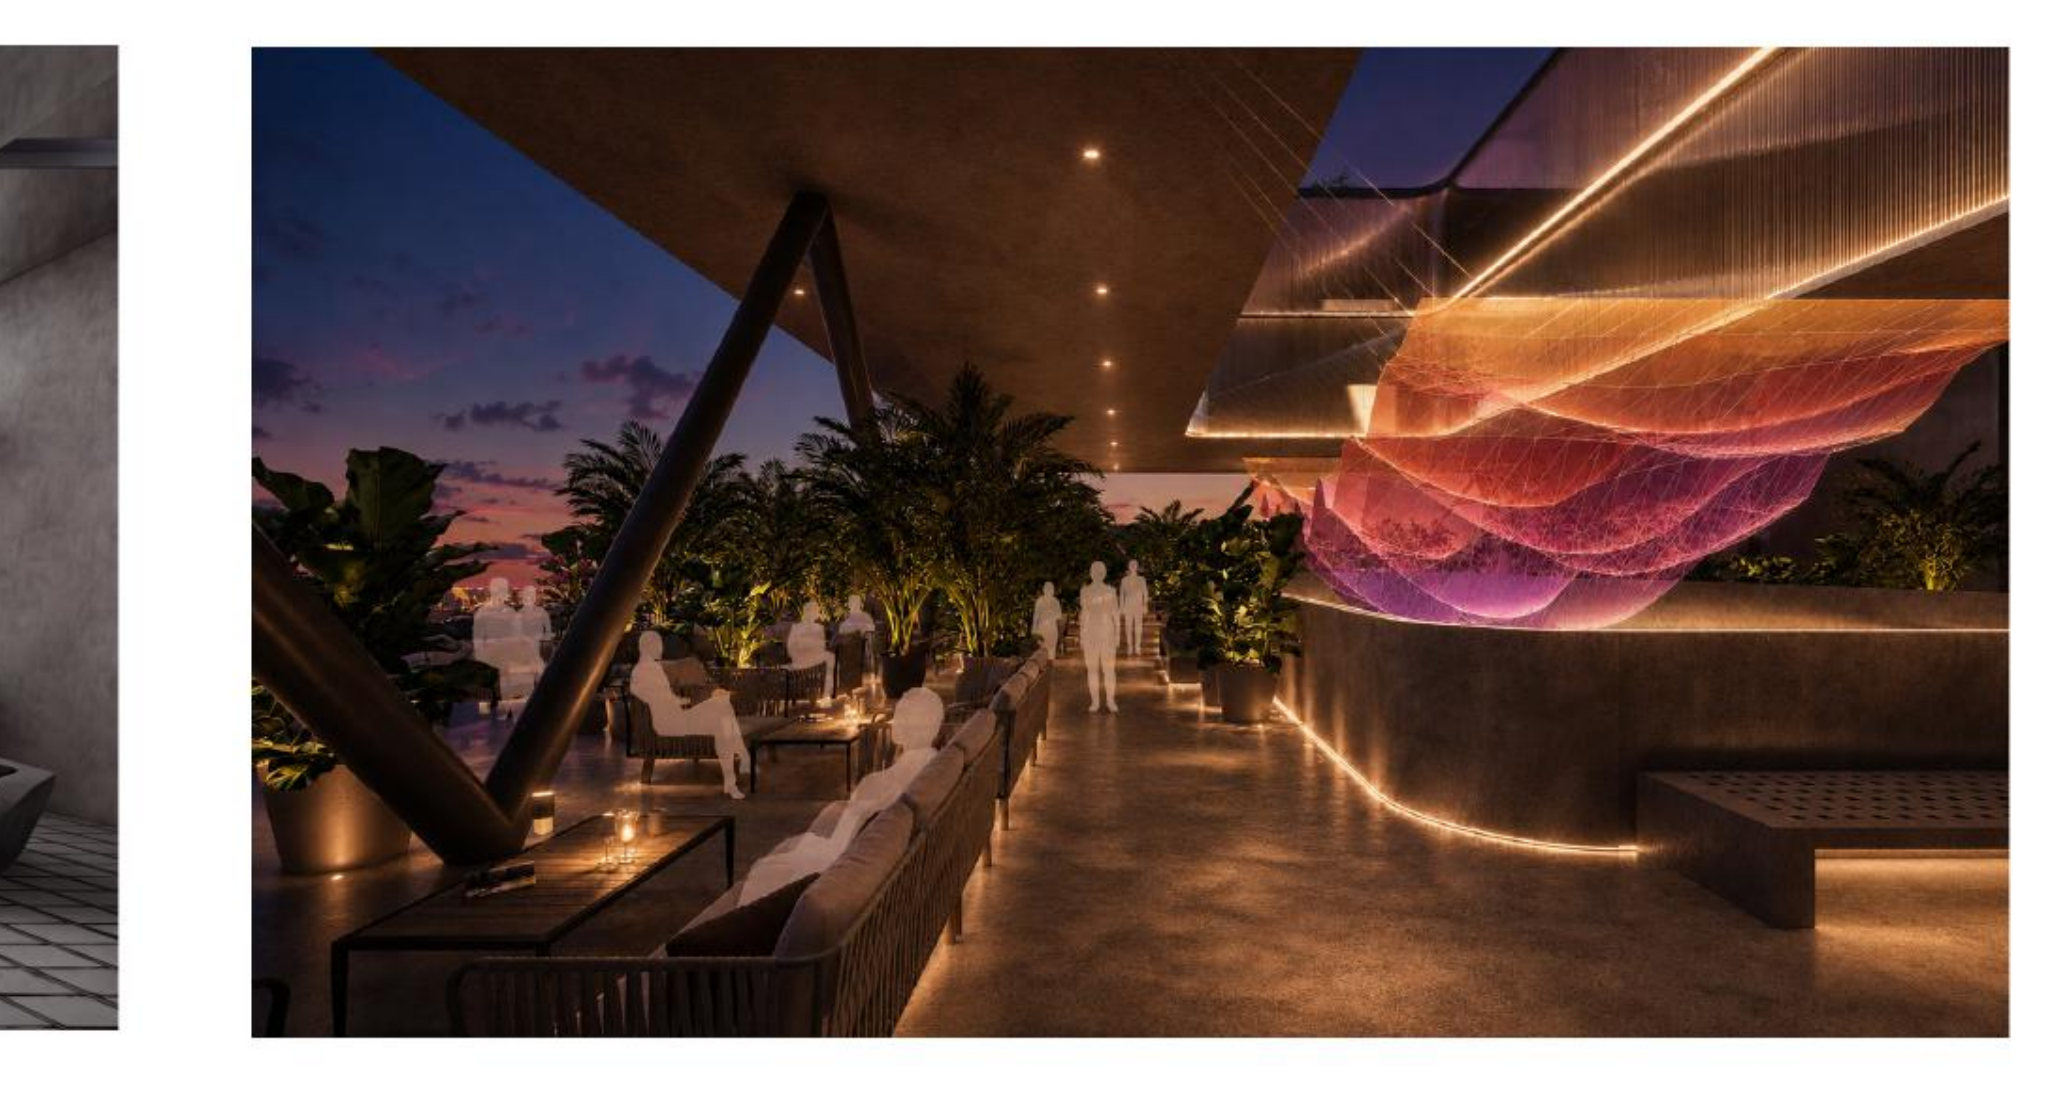

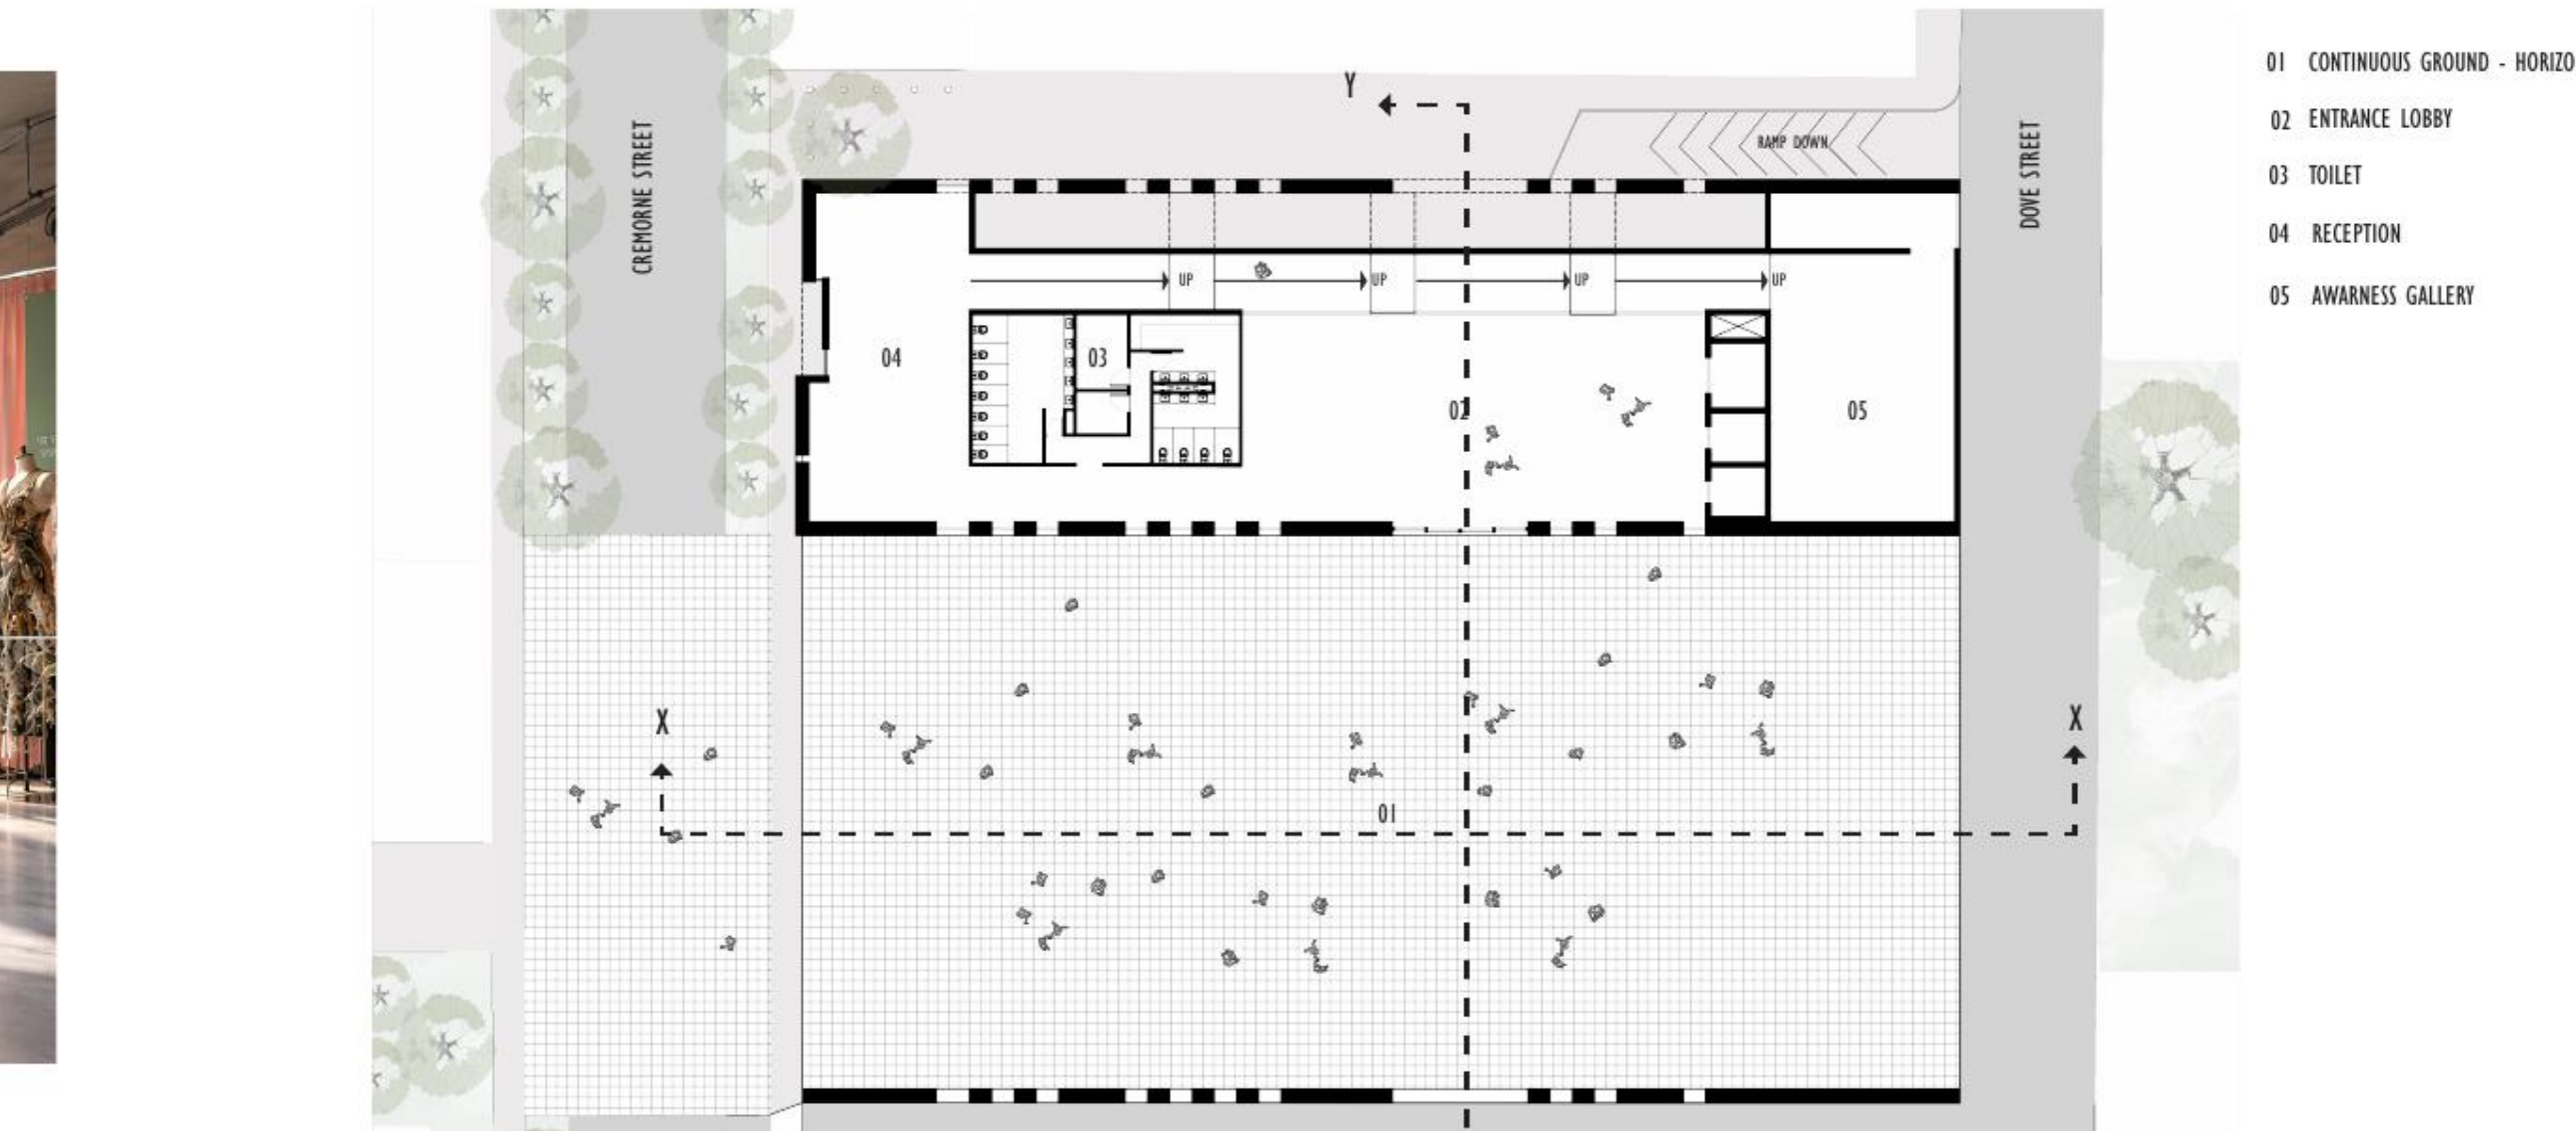
CREMORNE STREET
DOVE STREET
RAMP DOWN
Y
X
01
03
04
05
N
0 1 2 3 4 5 10M

GROUND FLOOR PLAN

01 CONTINUOUS GROUND - HORIZONTAL
02 ENTRANCE LOBBY
03 TOILET
04 RECEPTION
05 AWARNESS GALLERY

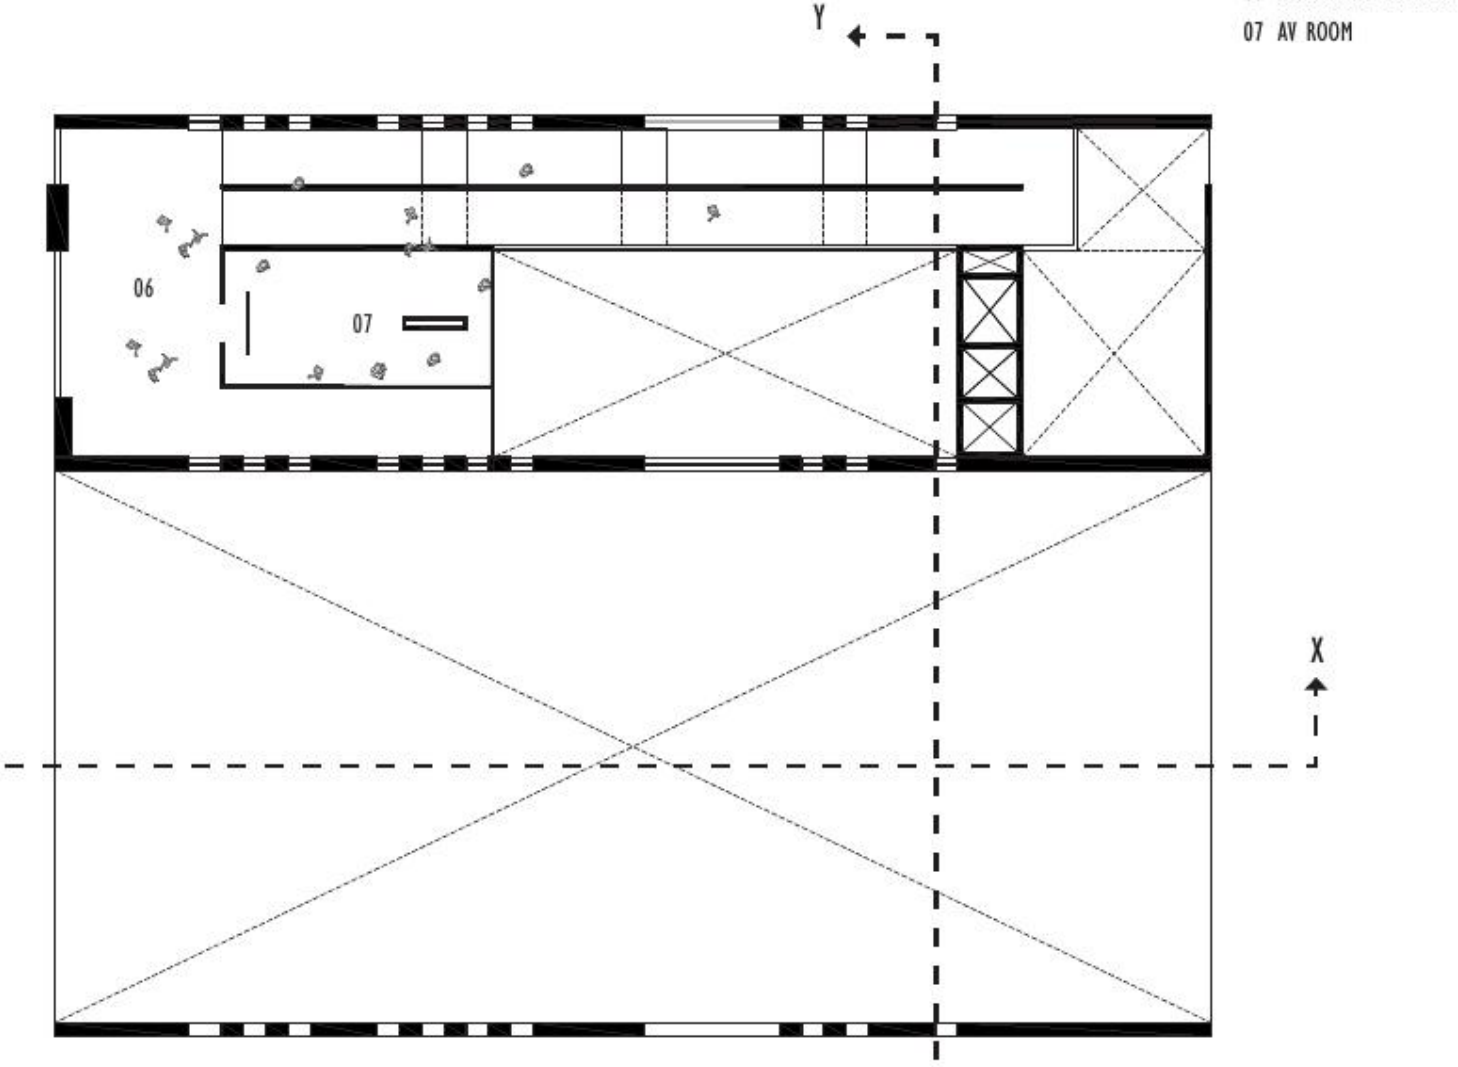

06 AWARENESS GALLERY
07 AV ROOM

FIRST FLOOR PLAN

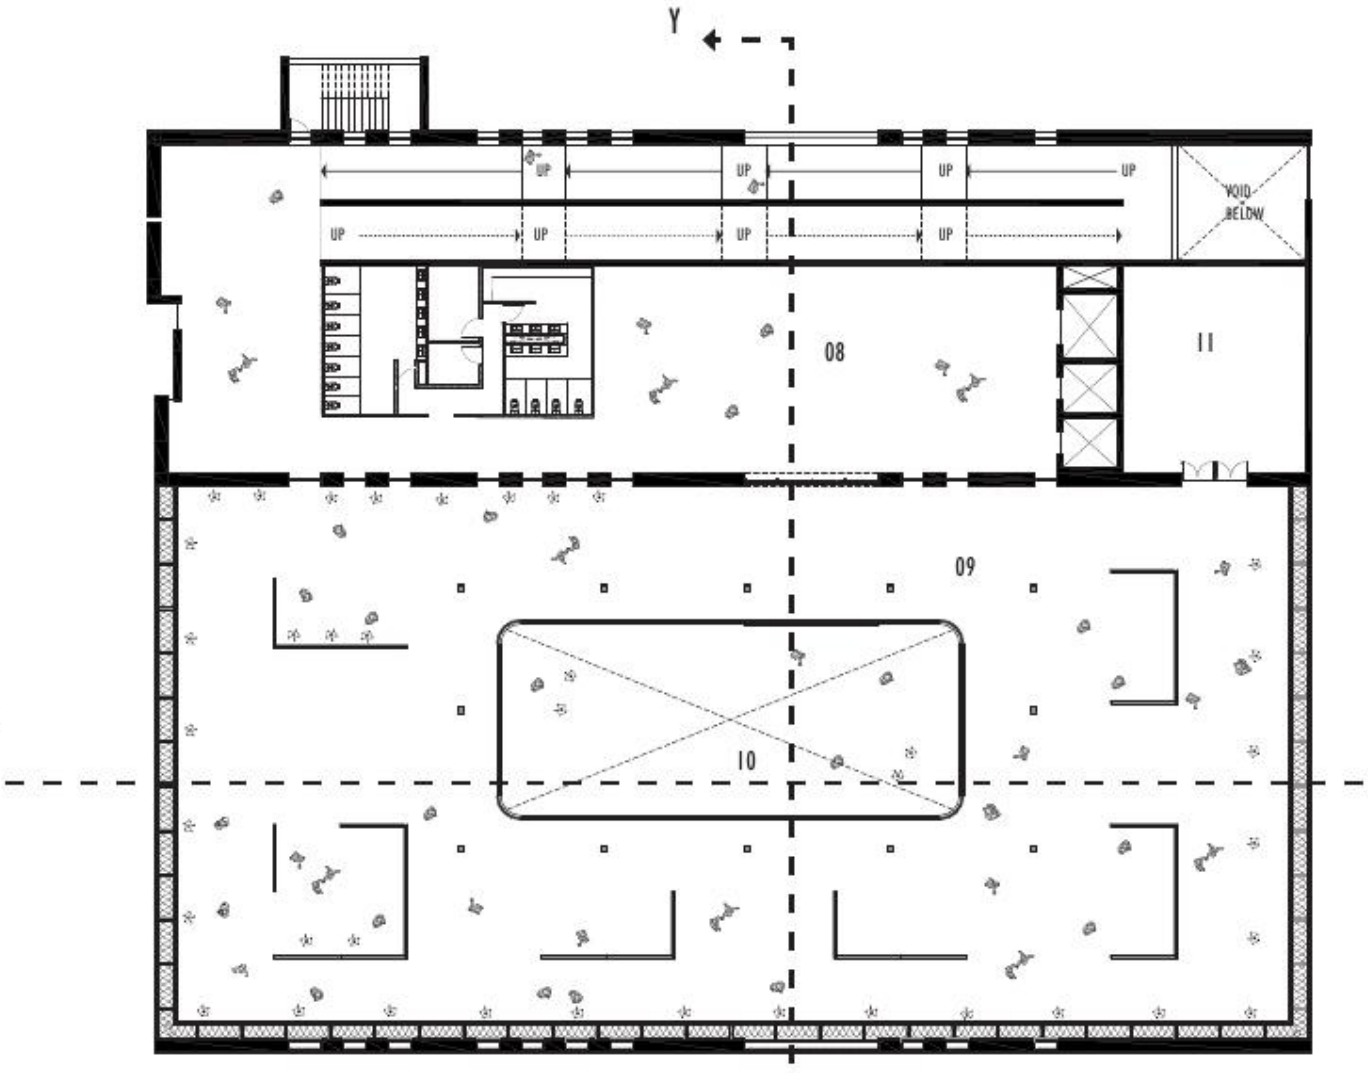
Y
X
08
09
10
11

08 EXHIBITION SPACE 01
09 EXHIBITION SPACE 02
10 ATRIUM
11 STORAGE

SECOND FLOOR PLAMN

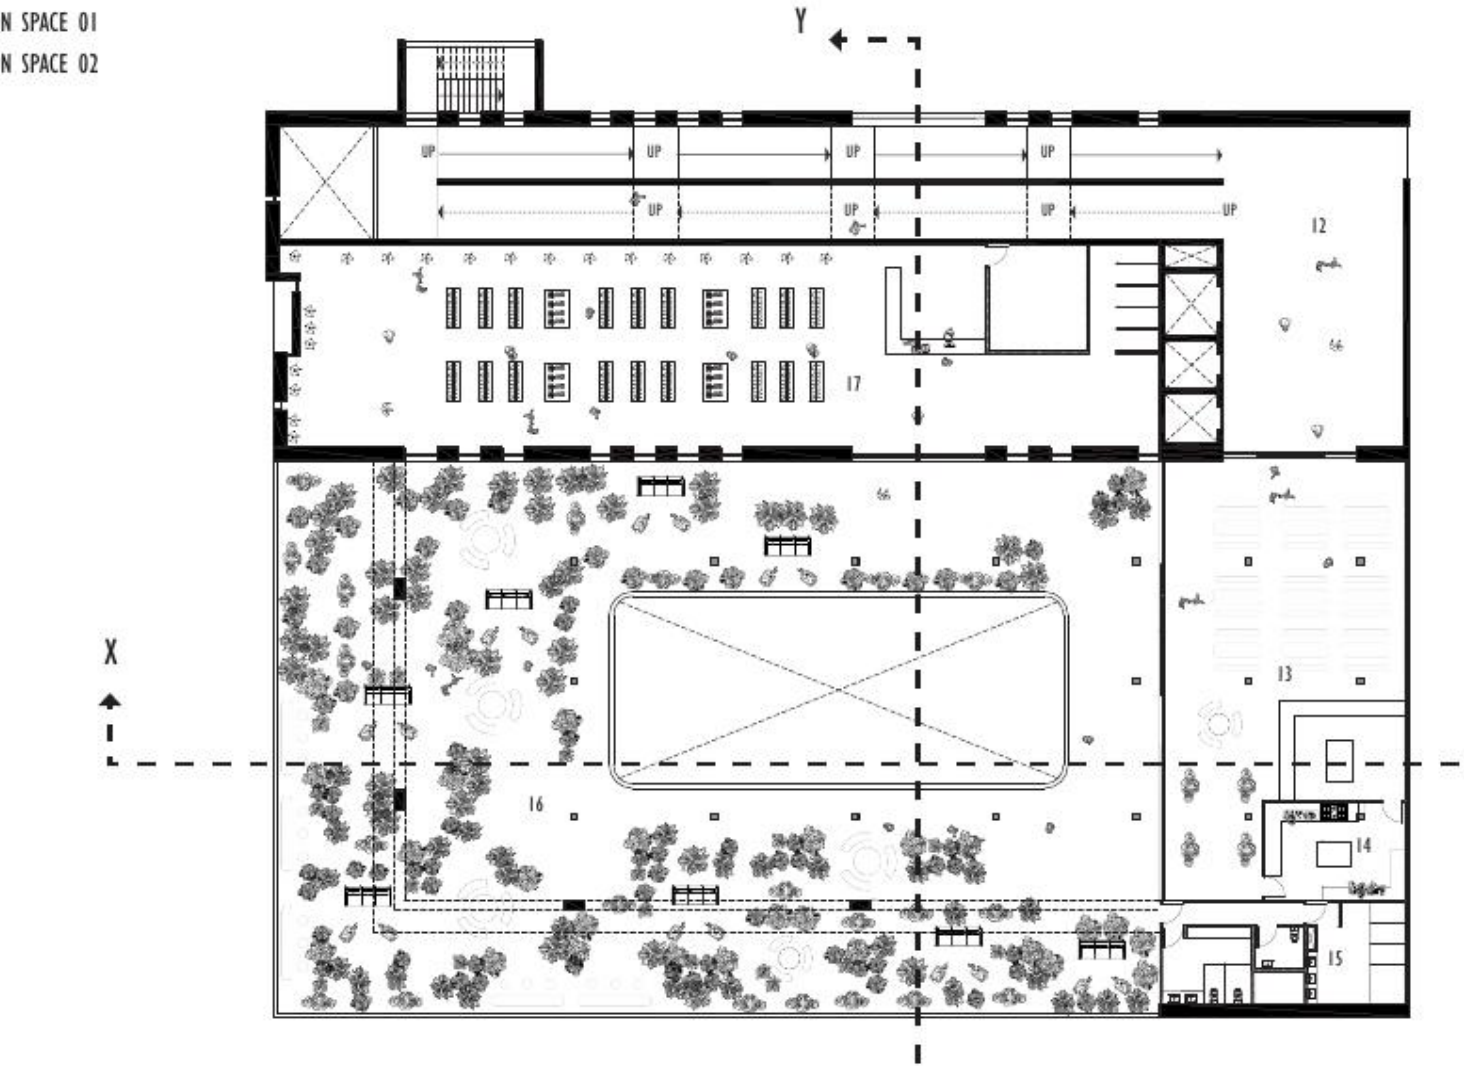
Y
X
12
13
14
15
16
17

12 LOBBY
13 CAFE / RESTAURANT
14 KITCHEN
15 TOILETS
16 PUBLIC GREEN SPACE
17 DESIGNER SHOPS

THIRD FLOOR PLAMN

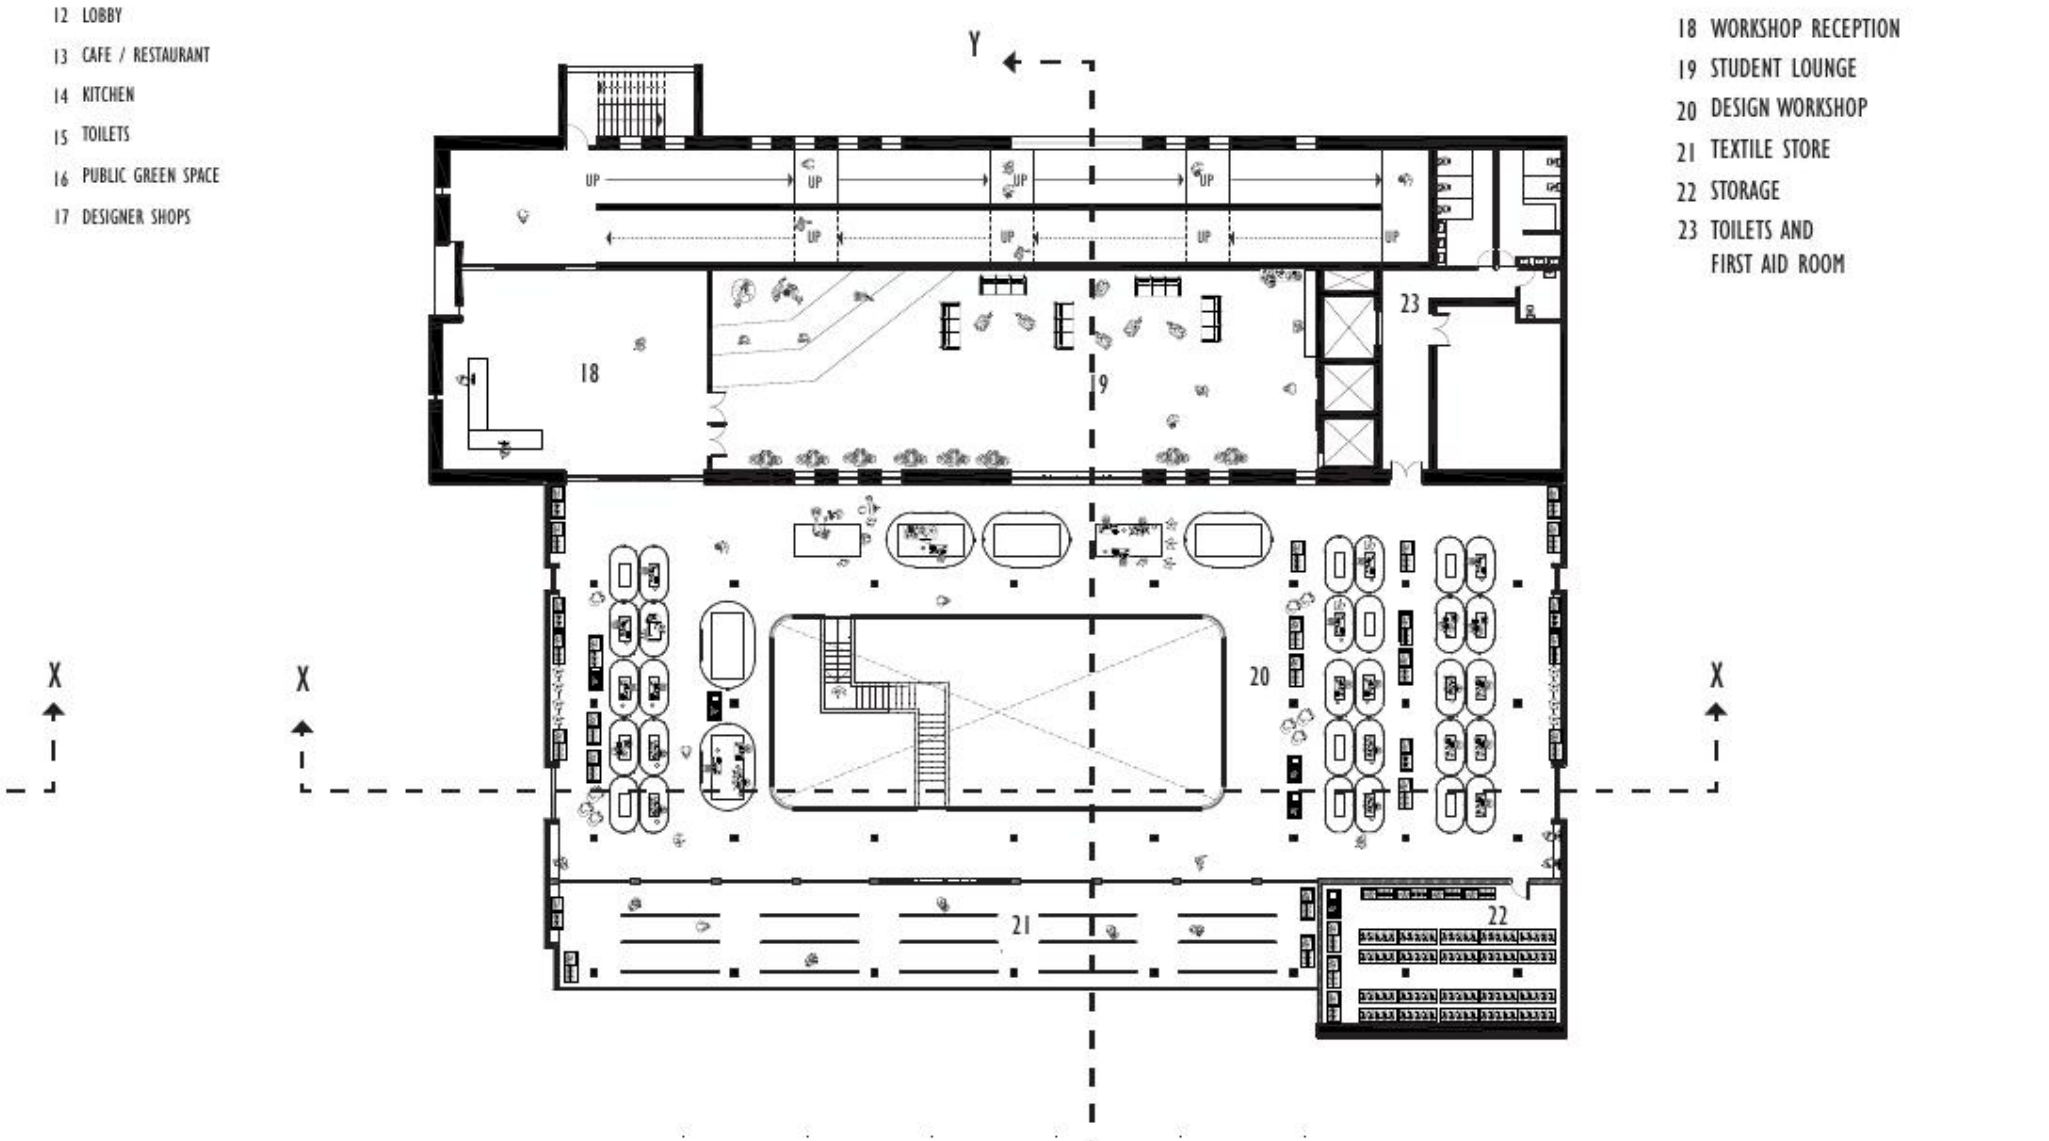
Y
X
18
19
20
21
22
23

18 WORKSHOP RECEPTION
19 STUDENT LOUNGE
20 DESIGN WORKSHOP
21 TEXTILE STORE
22 STORAGE
23 TOILETS AND
FIRST AID ROOM

FOURTH FLOOR PLAN

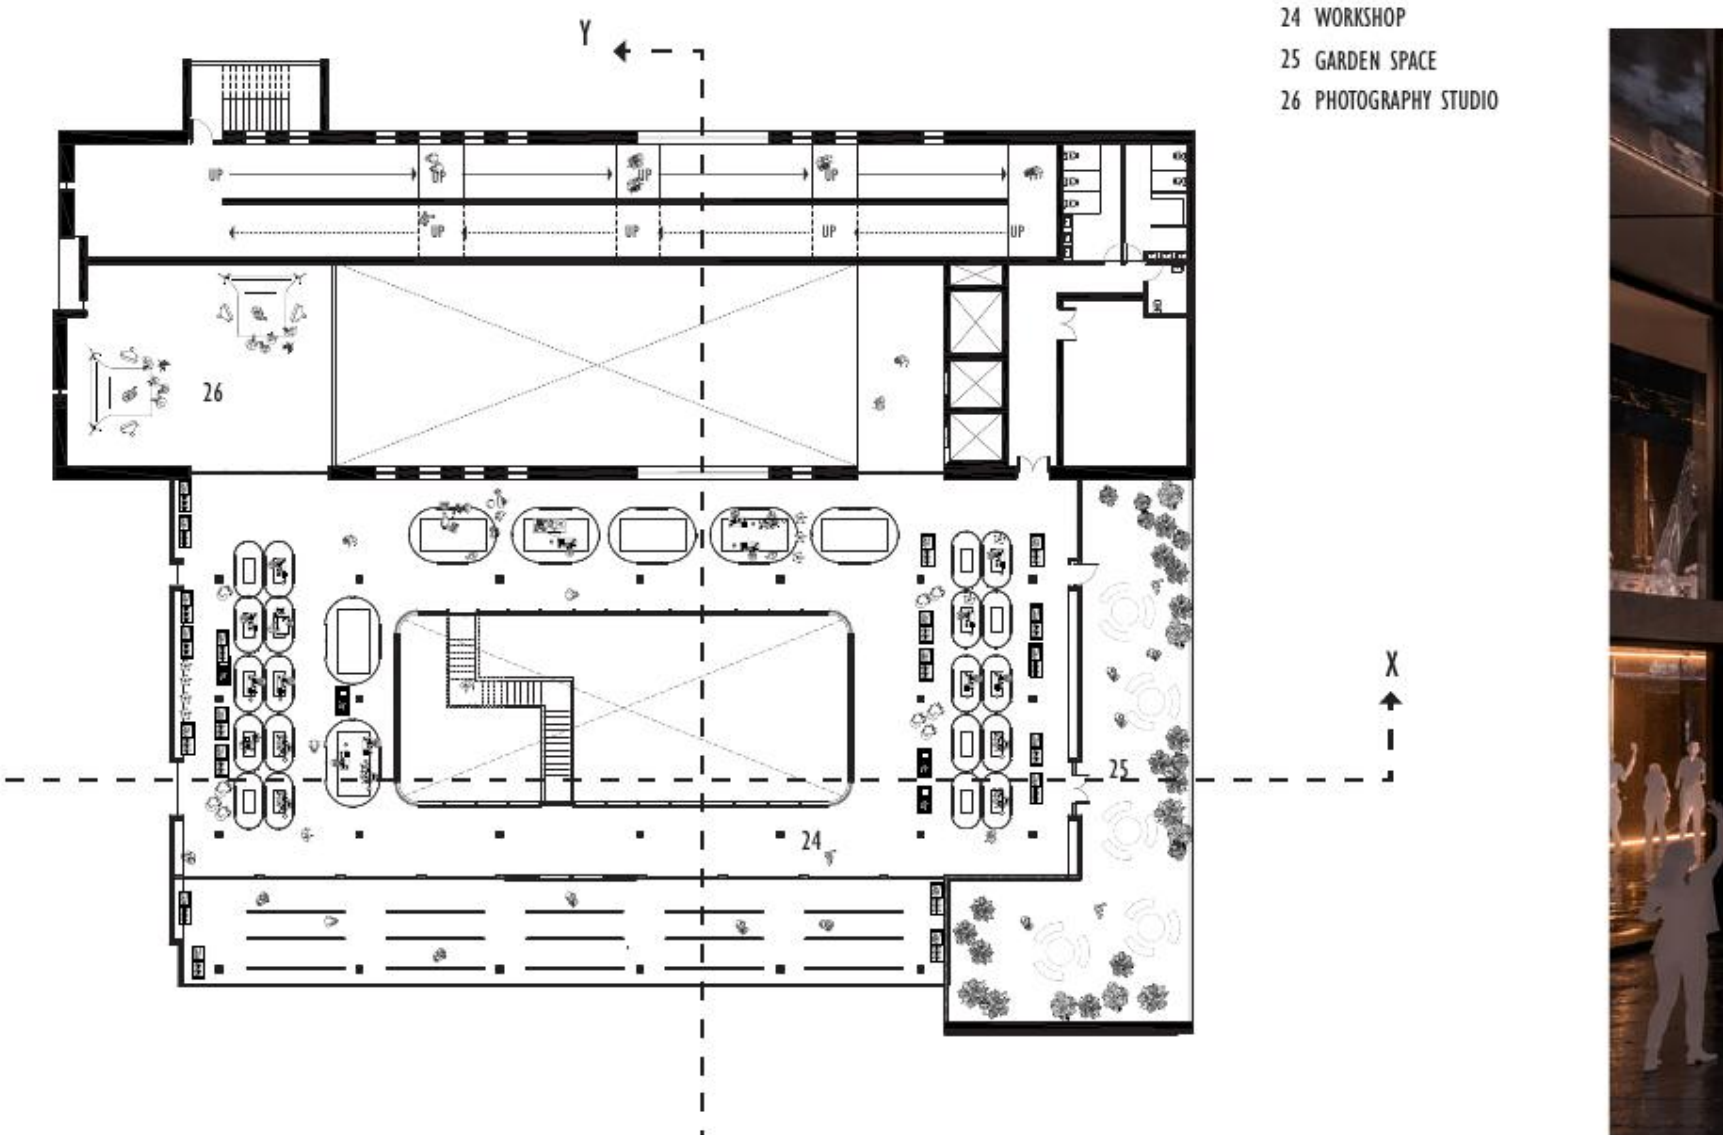
Y
X
24
25
26
N
0 1 2 3 4 5 10M

24 WORKSHOP
25 GARDEN SPACE
26 PHOTOGRAPHY STUDIO

FIFTH FLOOR PLAN

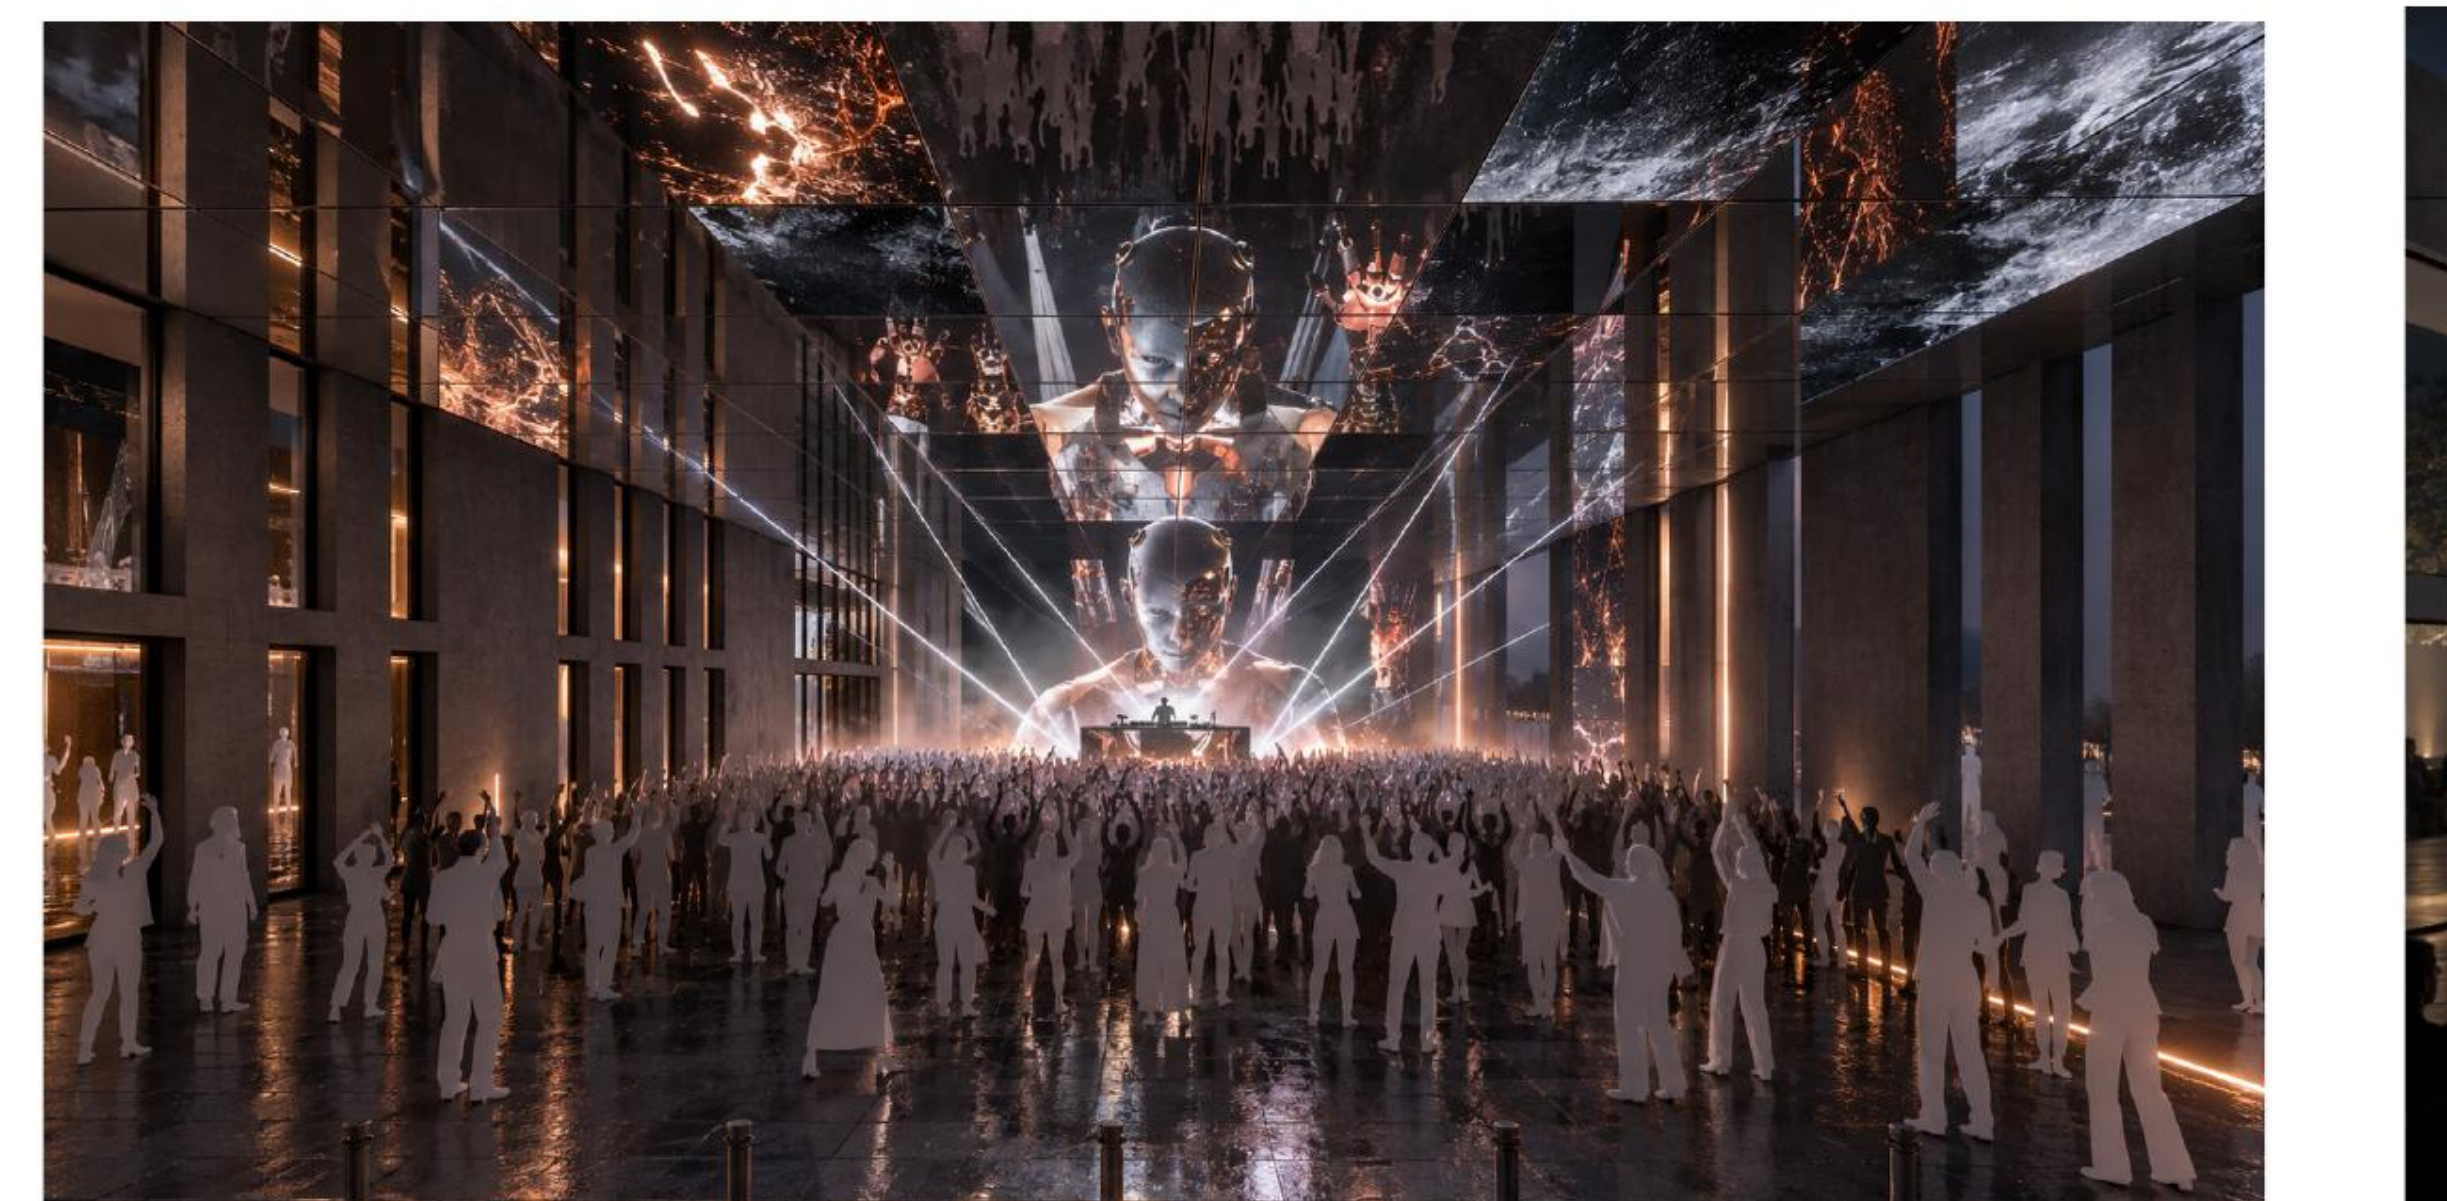

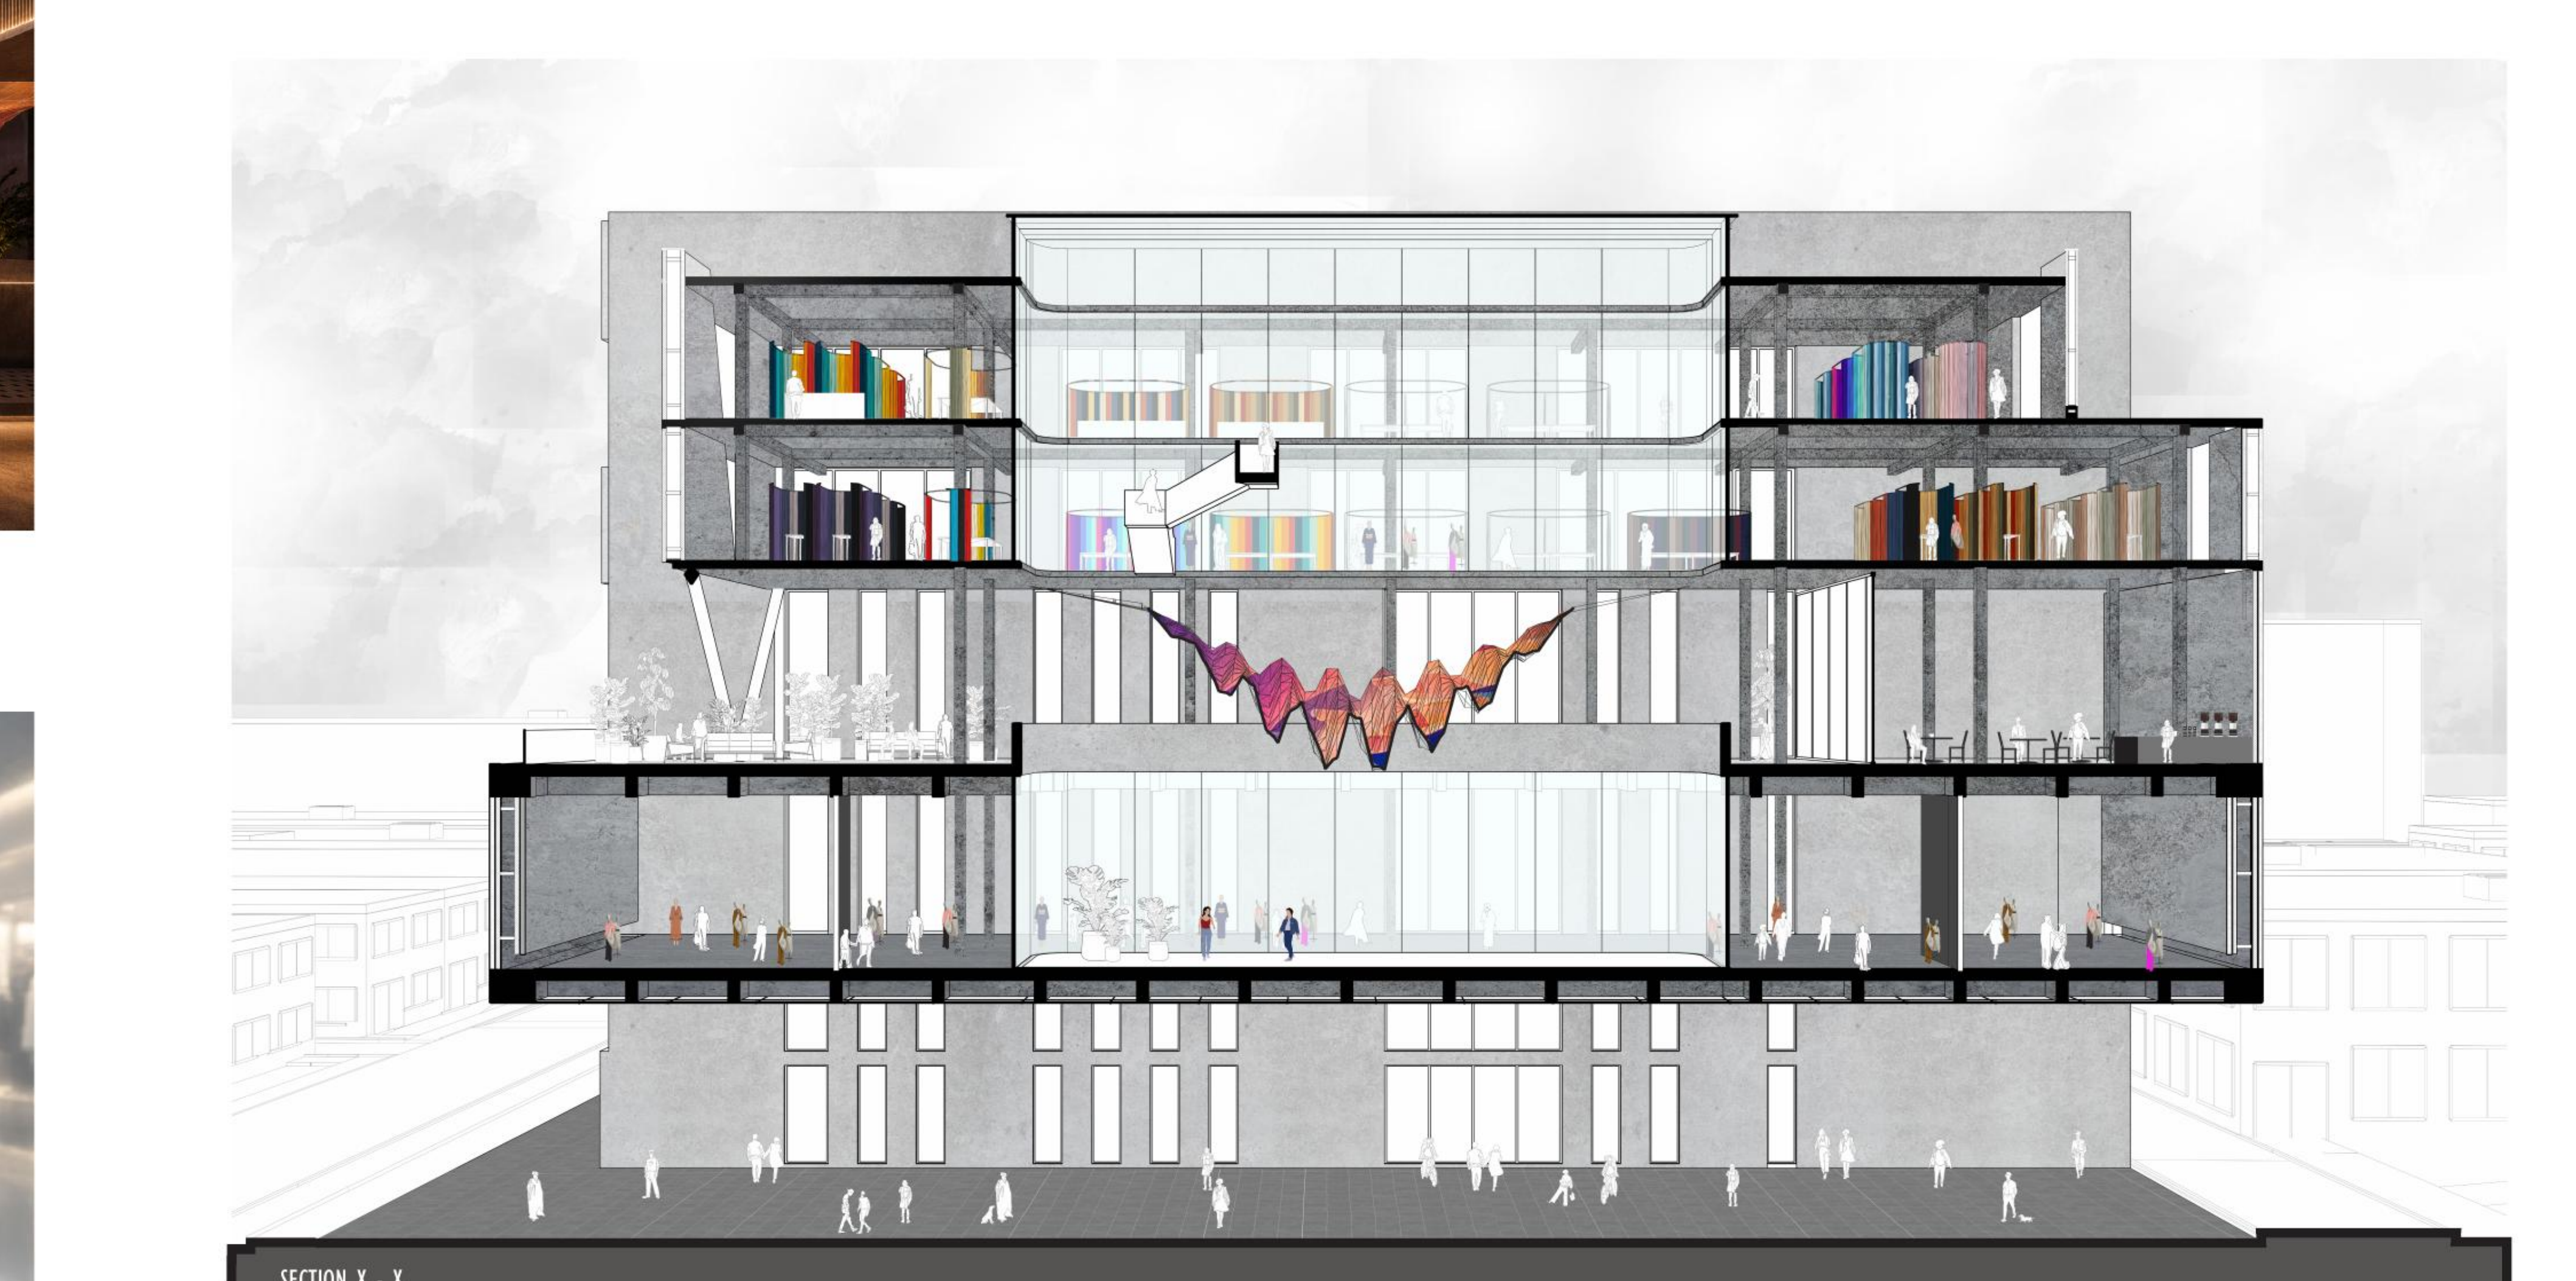

SECTION X - X
SCALE 1 : 100

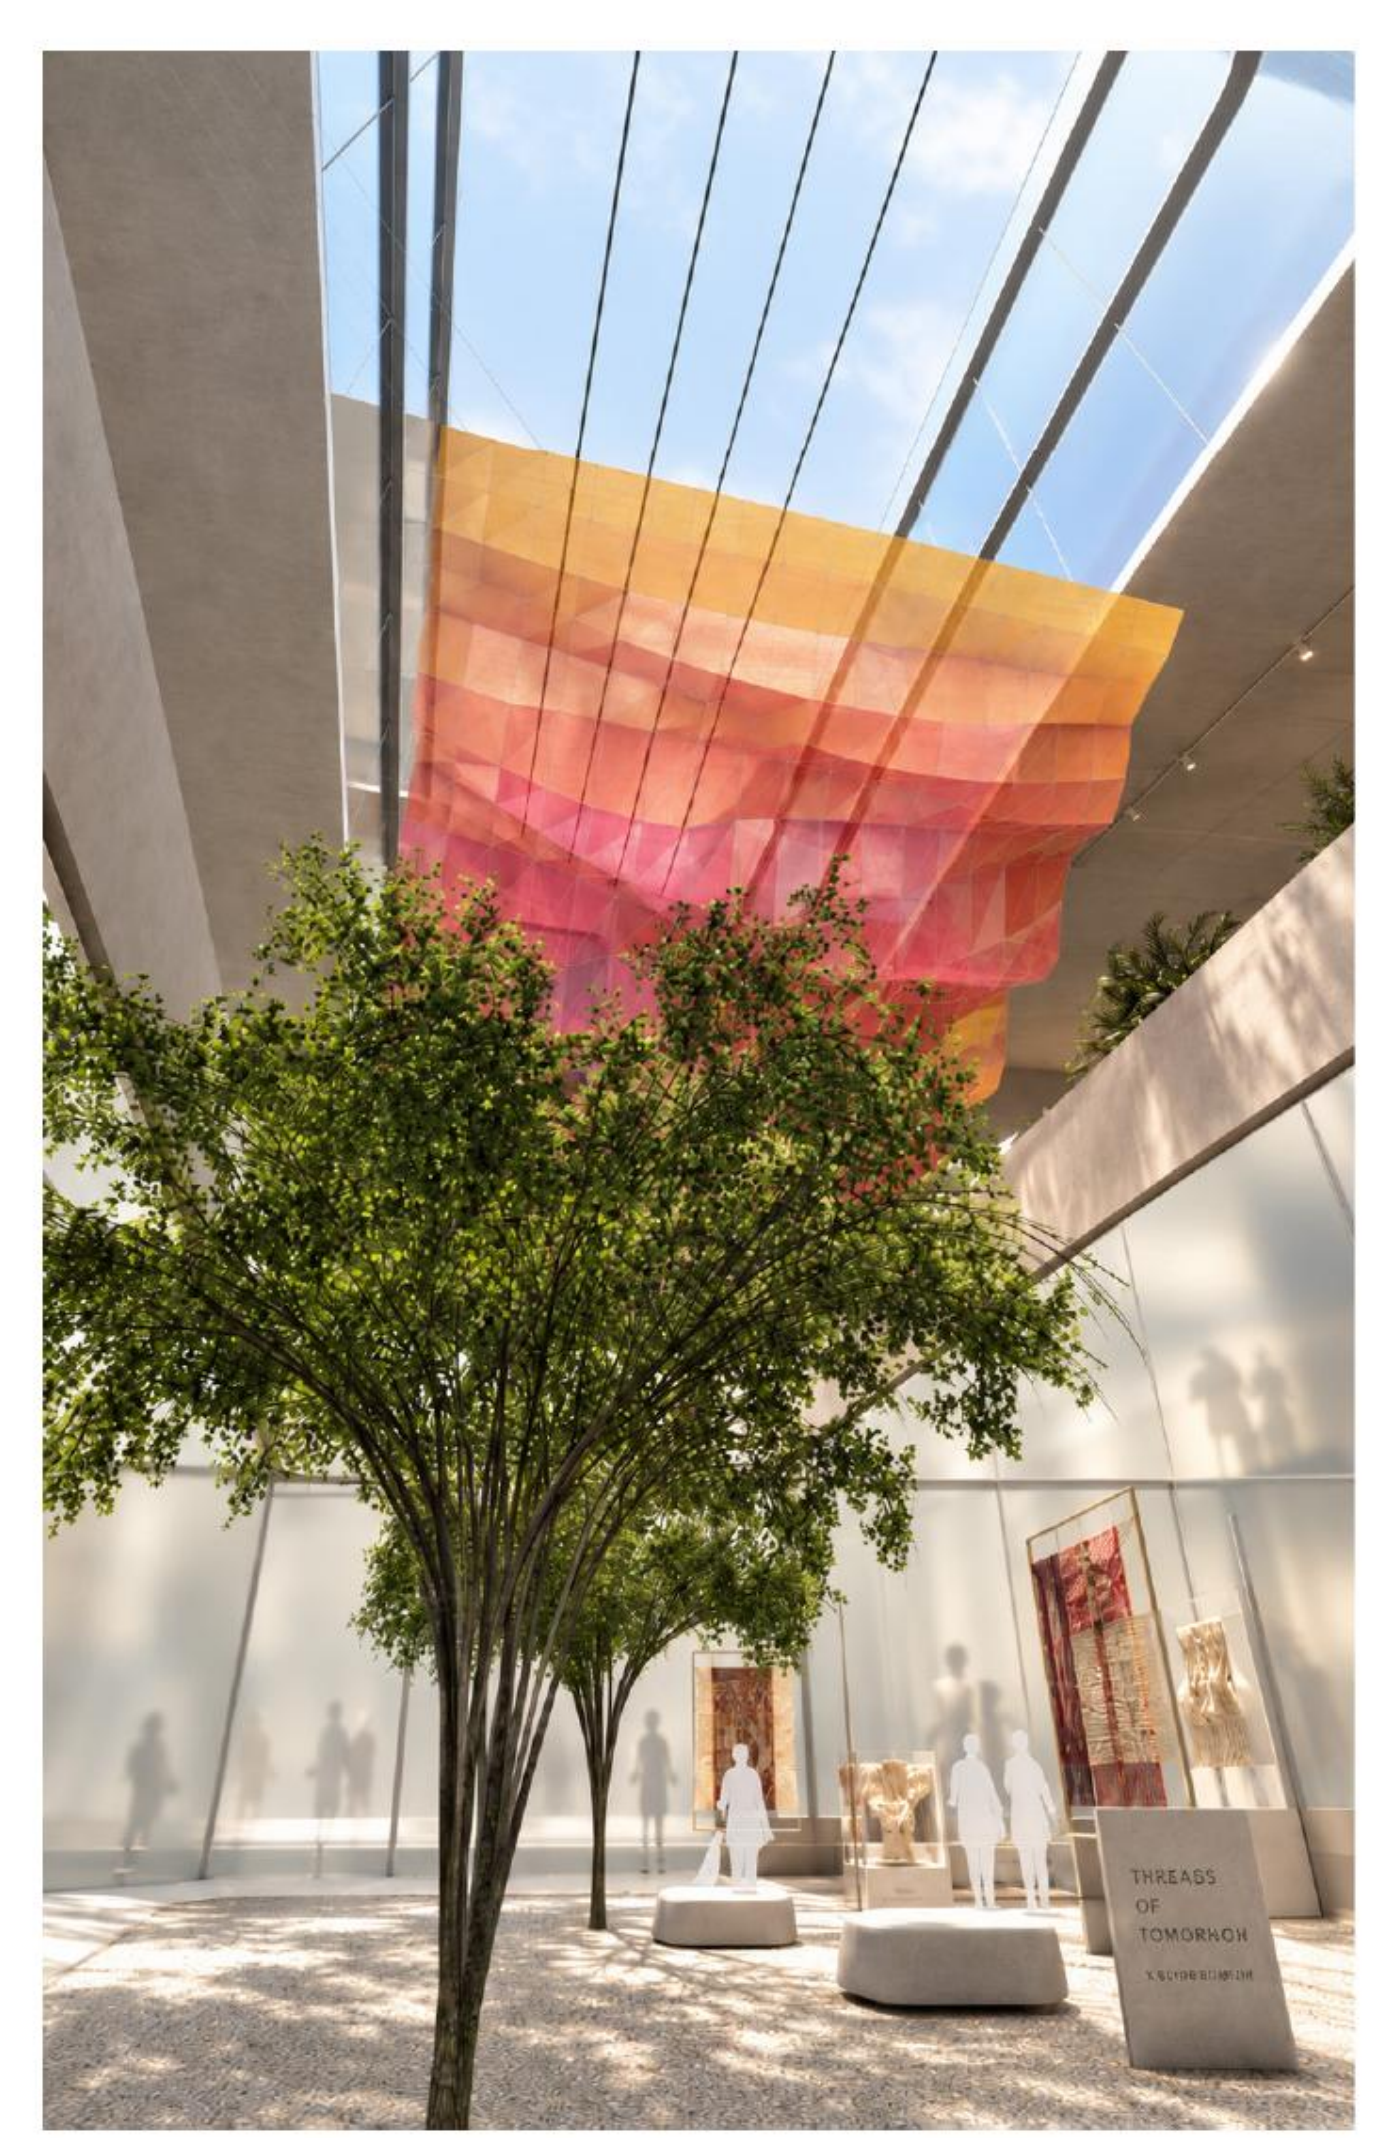
THREADS OF TOMORROW

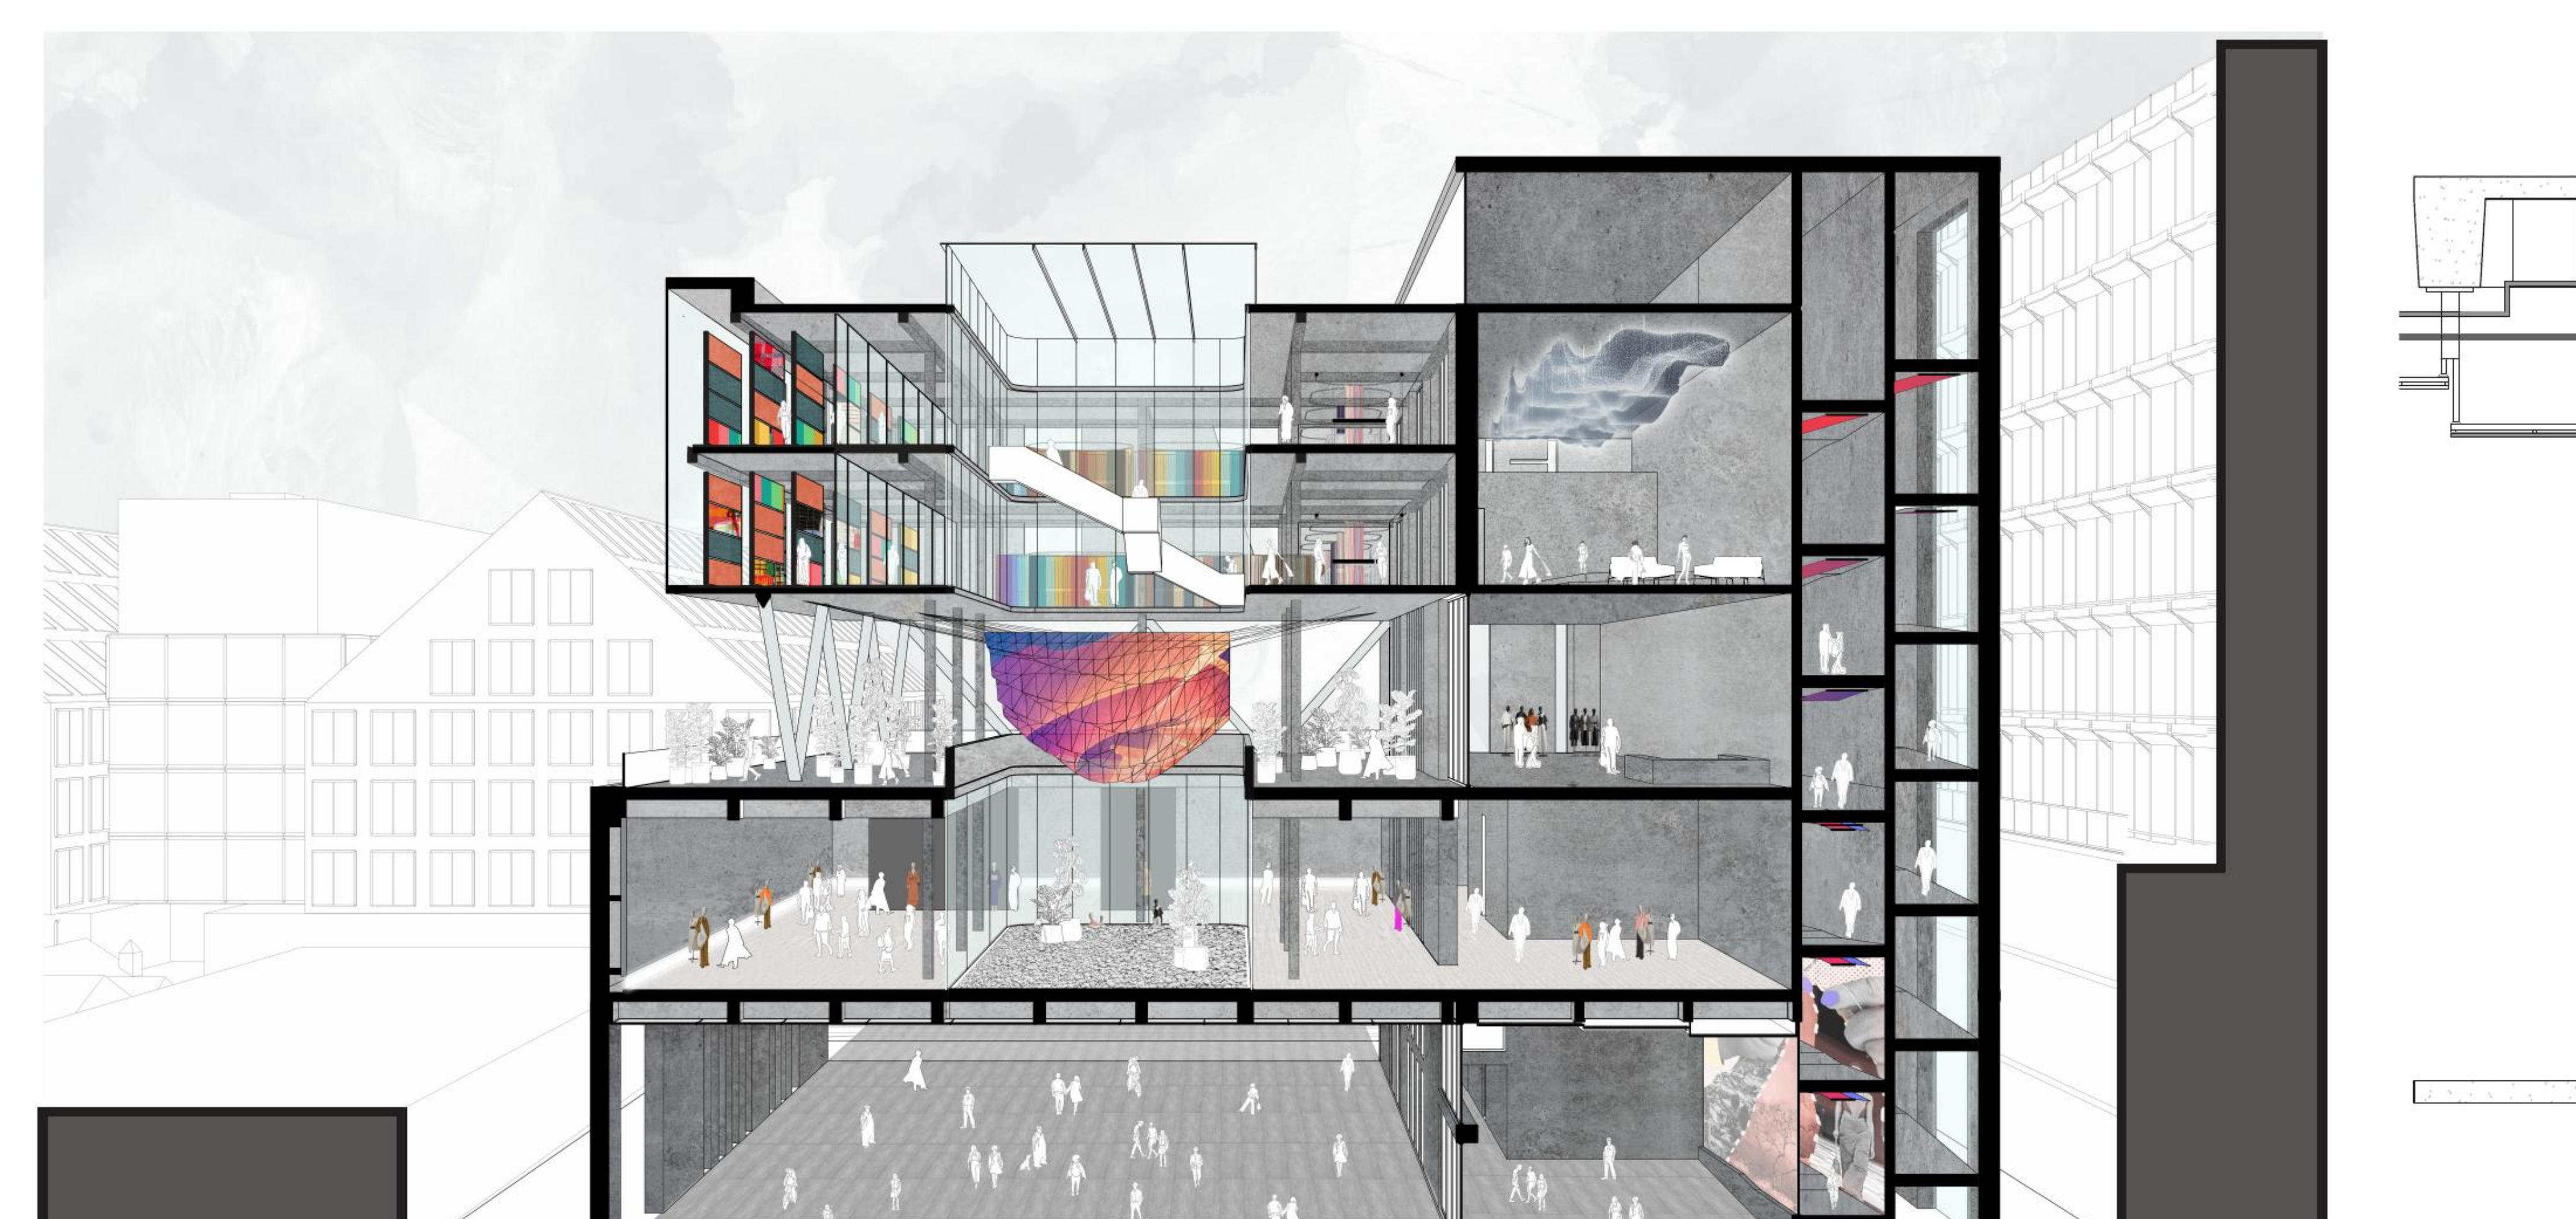

SECTION Y - Y
SCALE 1 : 100

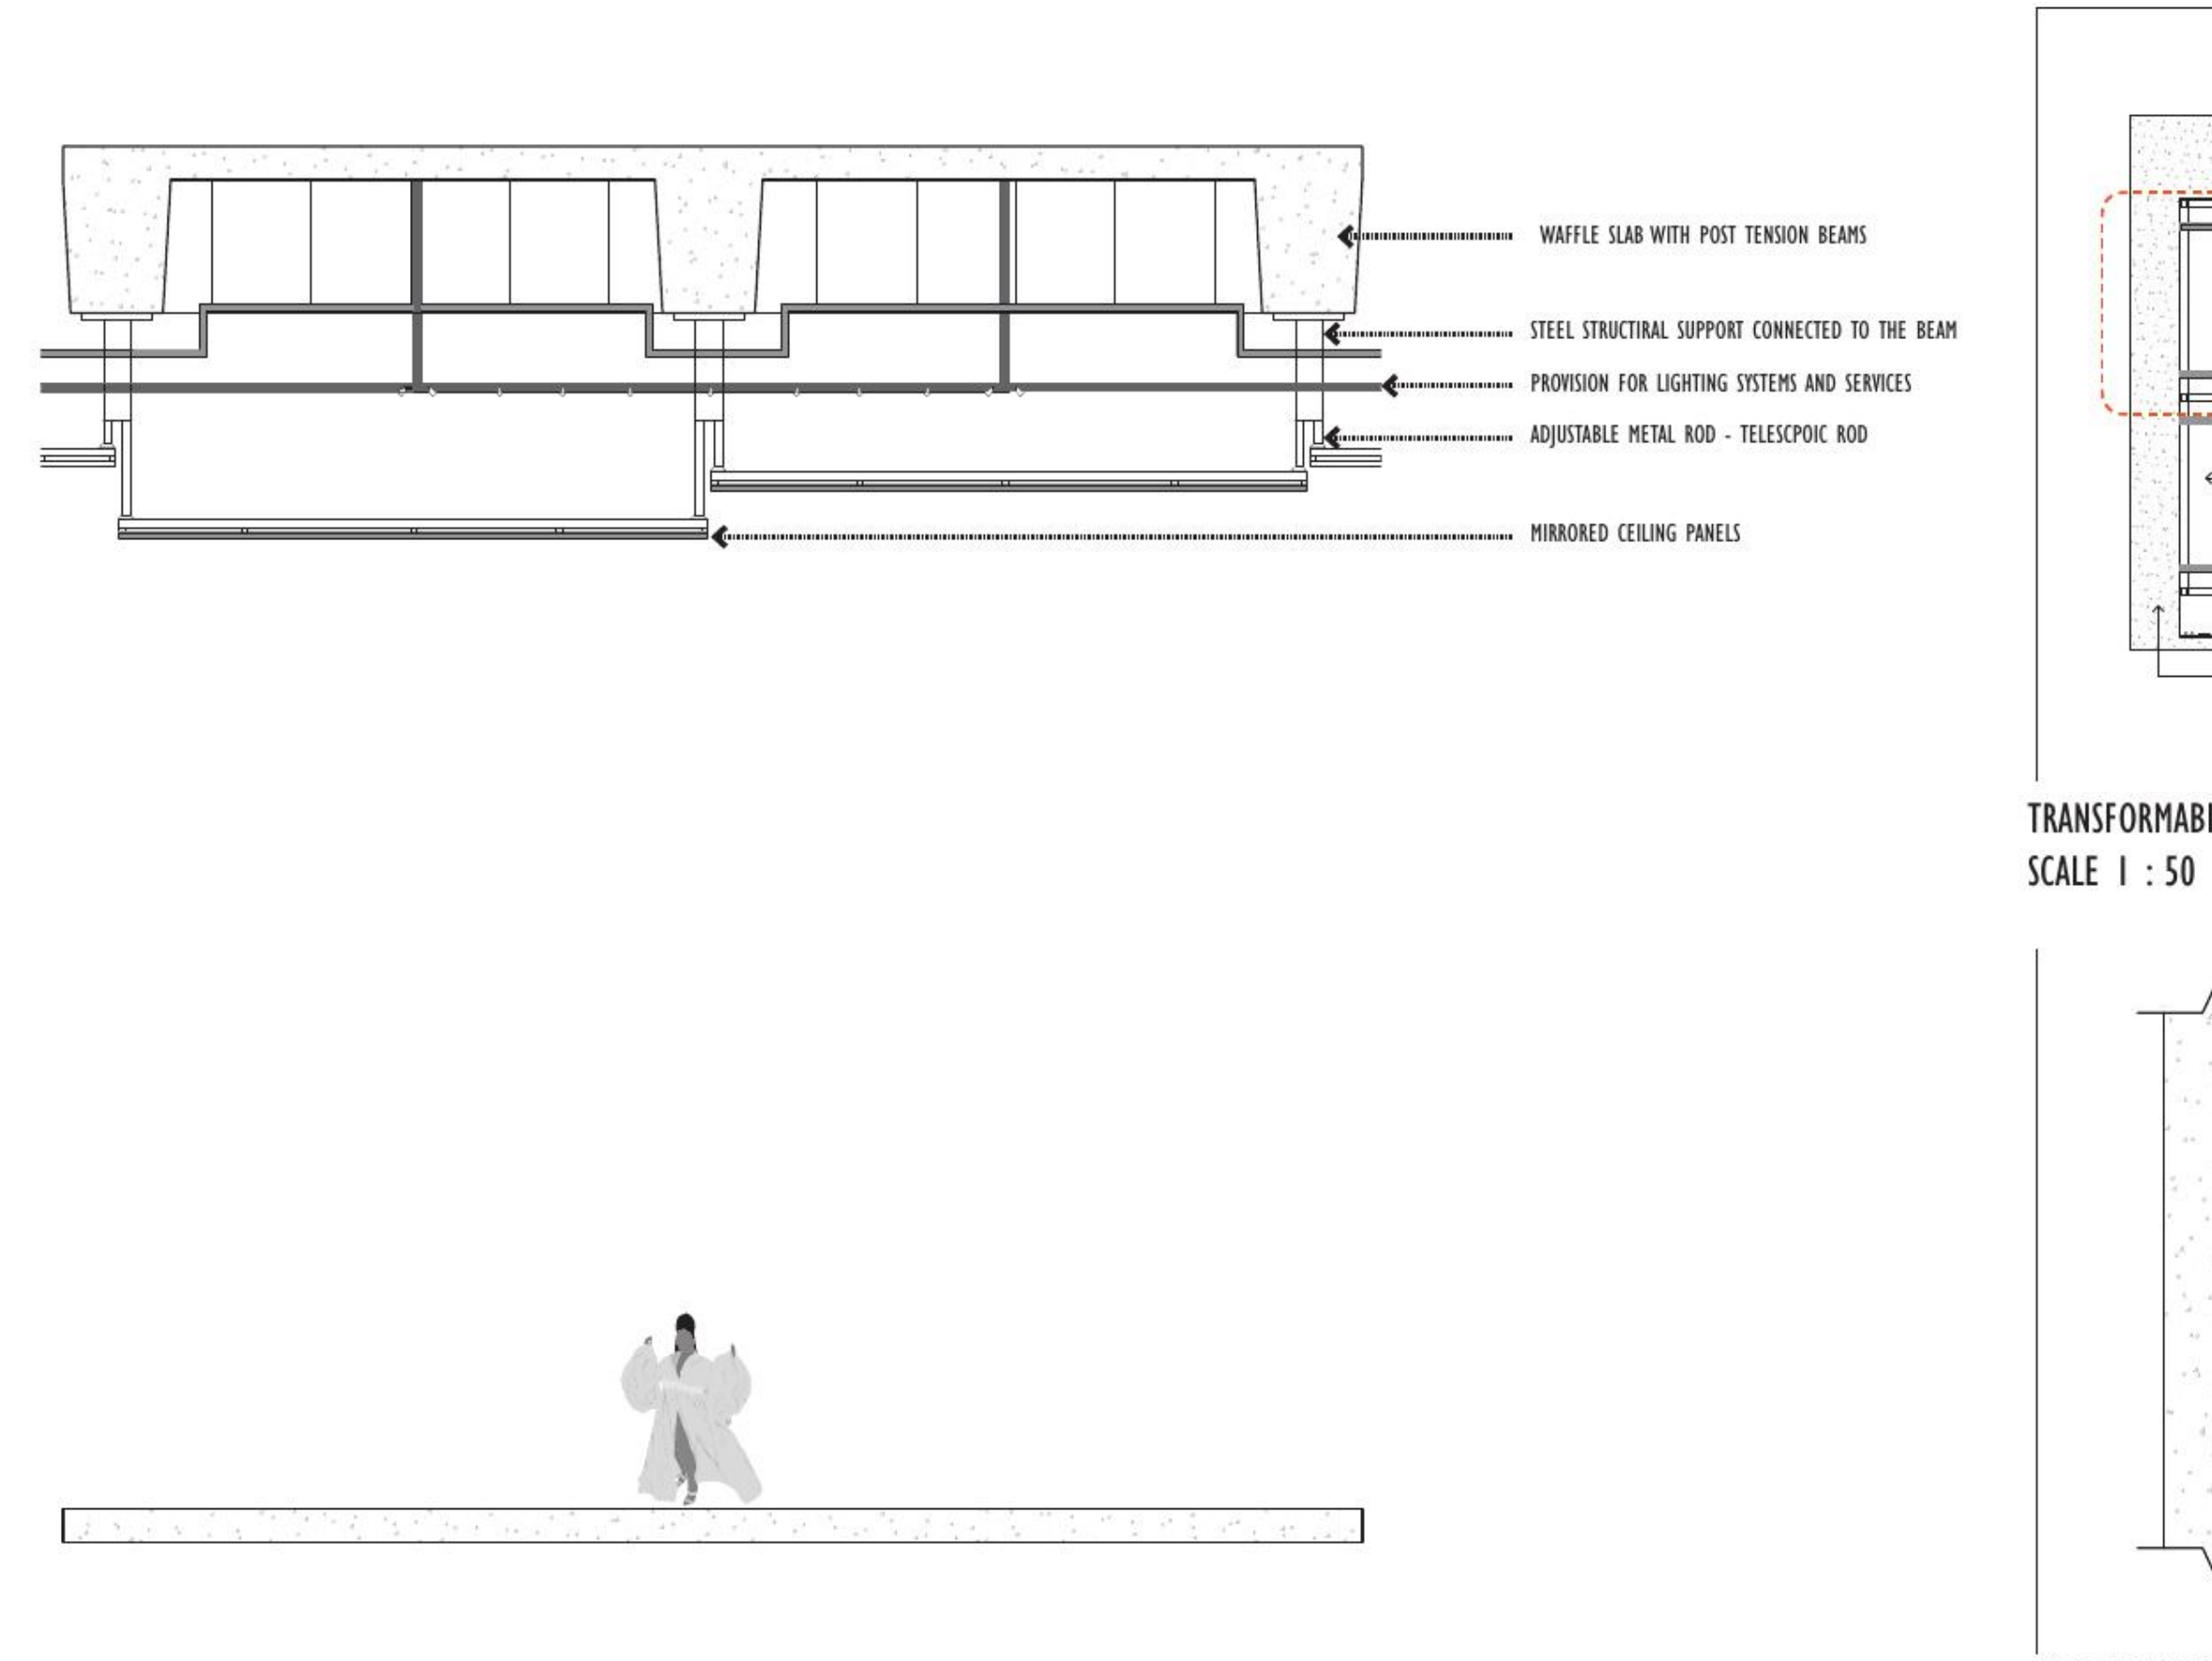
WAFFLE SLAB WITH POST TENSION BEAMS
STEEL STRUCTURAL SUPPORT CONNECTED TO THE BEAM
PROVISION FOR LIGHTING SYSTEMS AND SERVICES
ADJUSTABLE METAL ROD - TELESCPOIC ROD
MIRRORED CEILING PANELS

WAFFLE SLAB AND MIRRORED PANEL CONNECTION
SCALE 1 : 25

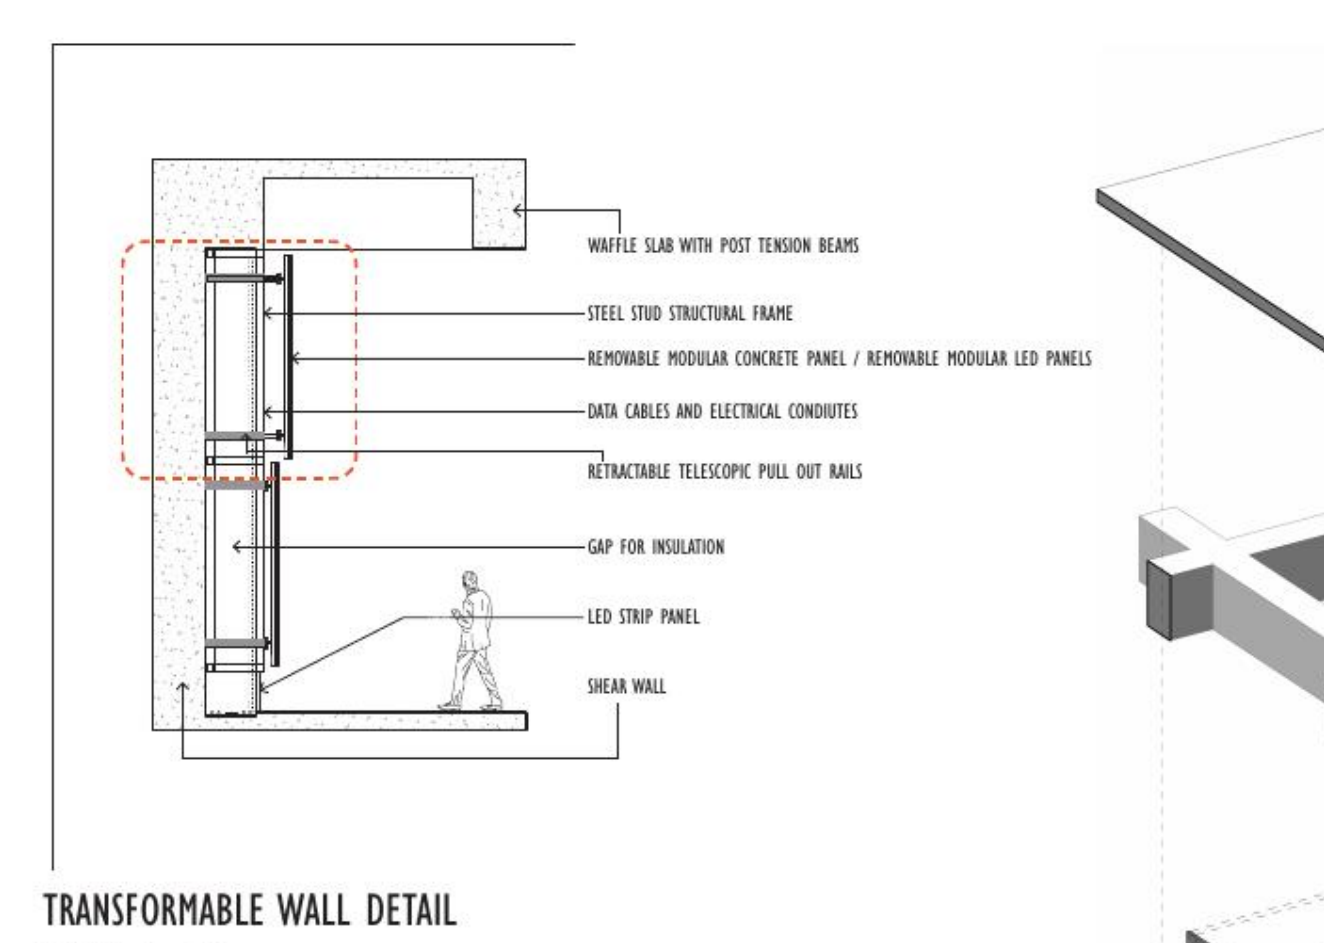
WAFFLE SLAB WITH POST TENSION BEAMS
STEEL STUD STRUCTURAL FRAME
REMOVABLE MODULAR CONCRETE PANEL / REMOVABLE MODULAR LED PANELS
DATA CABLES AND ELECTRICAL CONDUITS
RETRACTABLE TELESCOPIC PULL OUT RAILS
GAP FOR INSULATION
LED STRIP PANEL
SHEAR WALL

TRANSFORMABLE WALL DETAIL
SCALE 1 : 50

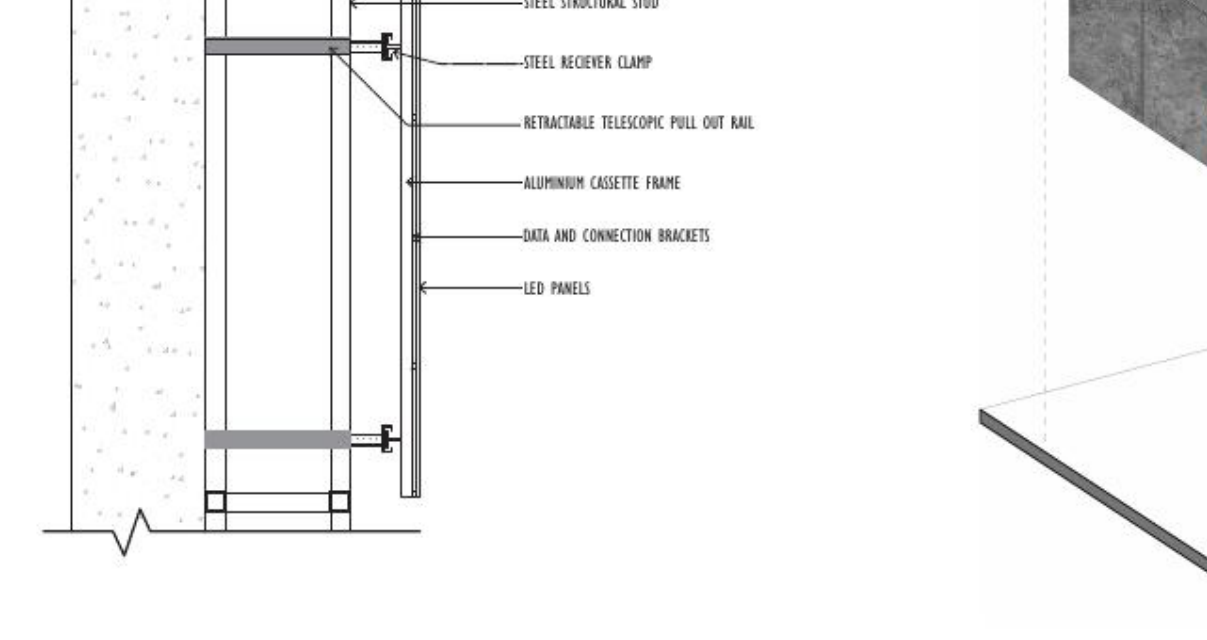
STEEL STRUCTURAL STUD
STEEL RECIEVER CLAMP
RETRACTABLE TELESCOPIC PULL OUT RAIL
ALUMINIUM CASSETTE FRAME
DATA AND CONNECTION BRACKETS
LED PANELS

TRANSFORMABLE WALL DETAIL
SCALE 1 : 20

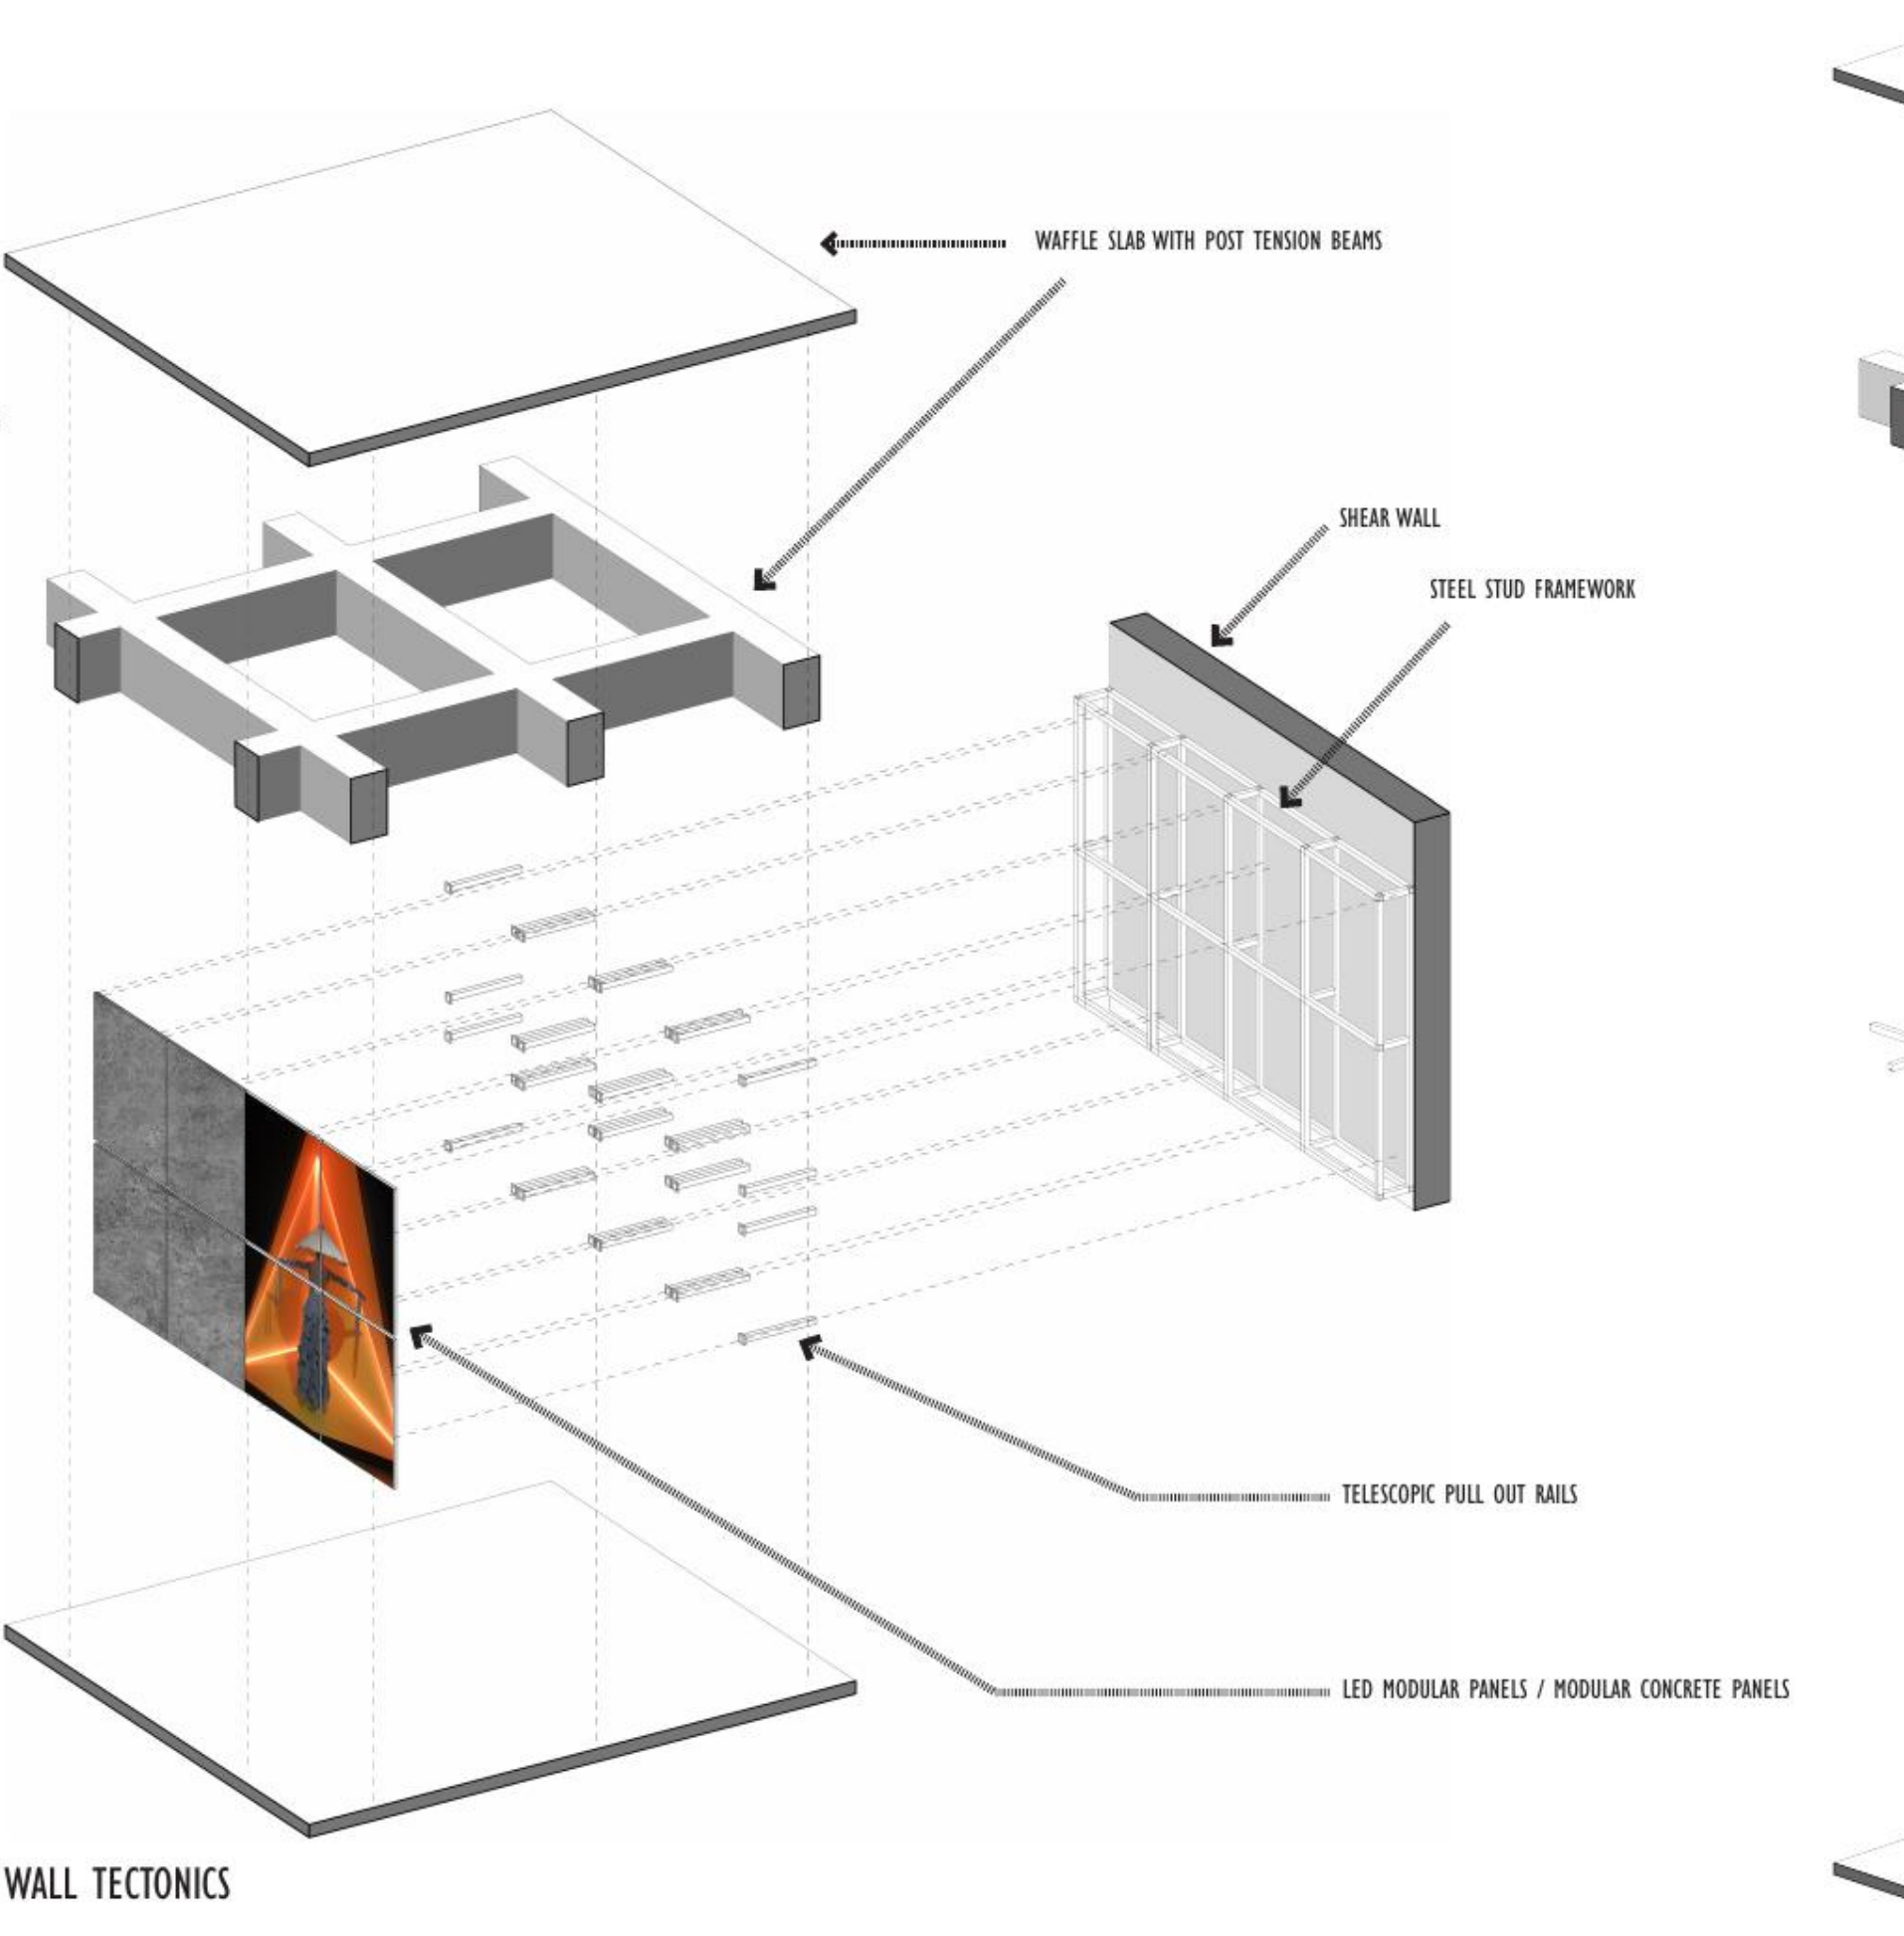
WAFFLE SLAB WITH POST TENSION BEAMS
SHEAR WALL
STEEL STUD FRAMEWORK
TELESCOPIC PULL OUT RAILS
LED MODULAR PANELS / MODULAR CONCRETE PANELS

WALL TECTONICS

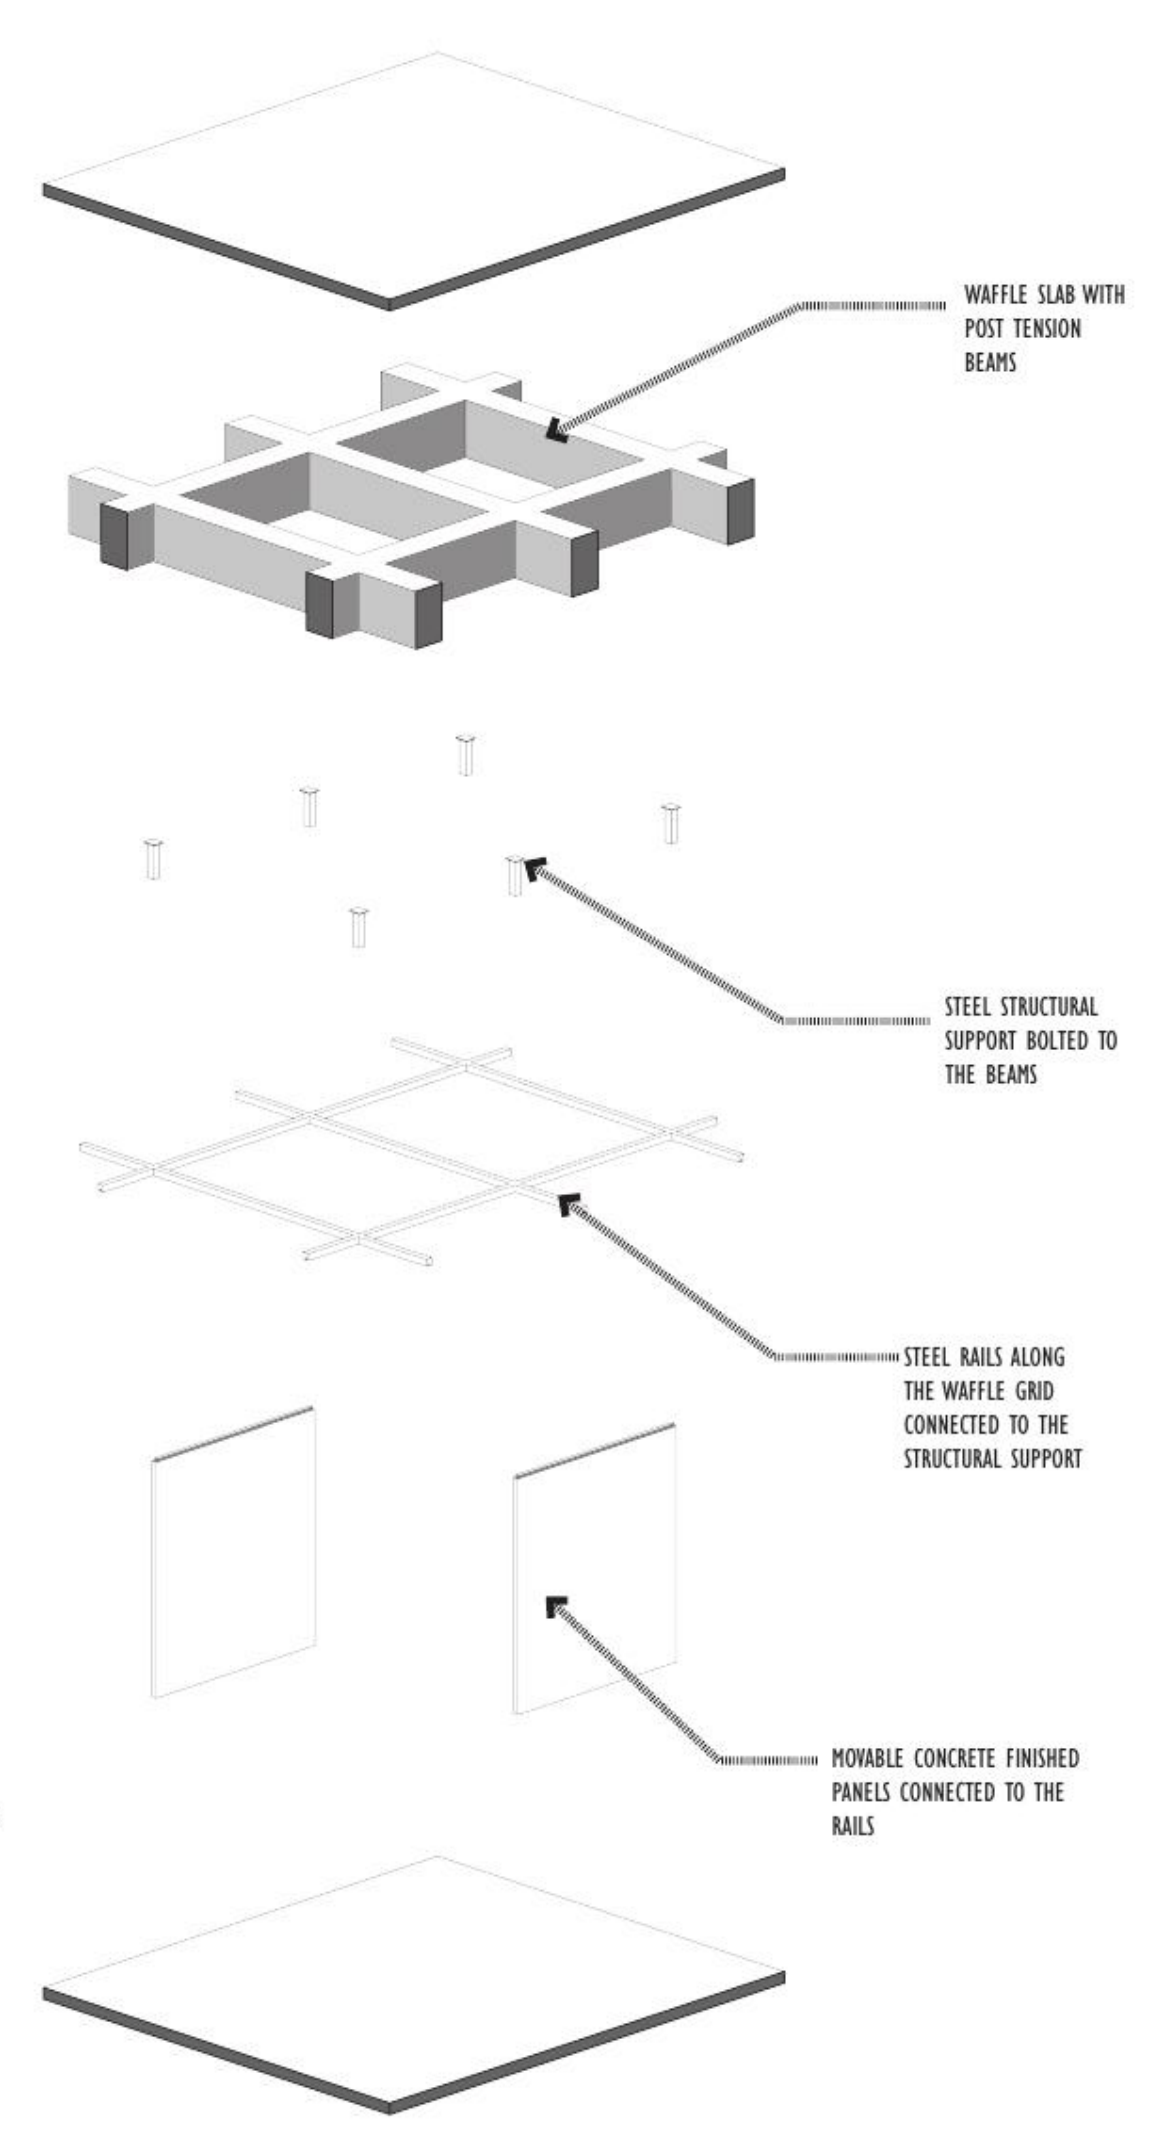
WAFFLE SLAB WITH POST TENSION BEAMS
STEEL STRUCTURAL SUPPORT BOLTED TO THE BEAMS
STEEL RAILS ALONG THE WAFFLE GRID CONNECTED TO THE STRUCTURAL SUPPORT
MOVABLE CONCRETE FINISHED PANELS CONNECTED TO THE RAILS